

ДИЗАЙН-ПРОЕКТ ИНТЕРЬЕРОВ АППАРТ-ОТЕЛЯ Холл-ресепшн

Адрес: г. Санкт-Петербург, ул. Херсонская д.43/12, лит. А
Версия 13-08-2019



№041/АИ-0217

Проект выполнен студией архитектуры и дизайна maxdesign
Старо-Петергофский проспект 44, офис 310


Санкт-Петербург
2019г.

ВЕДОМОСТЬ ЧЕРТЕЖЕЙ

Ведомость чертежей основного комплекта марки АИ

№ ЛИСТА	НАИМЕНОВАНИЕ	ПРИМЕЧАНИЕ
1	Ведомость чертежей основного комплекта	
2	План расстановки мебели. Первый этап.	
3	План расстановки мебели. Второй этап.	
4	План демонтажа стен и переноса коммуникаций.	
5	План возведения перегородок.	
6	Схема перегородки в лифтовый холл.	
7	План размещения сантехнических приборов.	
8	План напольных покрытий.	
9	План полов с обогревом.	
10	План потолков.	
11	План расположения осветительных приборов.	
12	Схема привязки осветительных приборов к выключателям.	
13	План размещения электрических розеток и электровыводов.	
14	Развертки стен с 1-1 по 4-4.	
15	Развертки стен с 5-5 по 8-8.	
16	Развертки стен с 9-9 по 16-16.	
17	Развертки стен с 17-17 по 28-28.	
18	Обрамление лифтового портала	
19	Ведомость заполнения дверных проемов.	
20	Спецификация внутренних витражей	
21	Спецификация оборудования и материалов.	
22	Спецификация цветов	

						05/2019г.			№ 04 1/ АИ-0217			
						Объект: апарт-отель. Адрес: г. Санкт-Петербург, ул. Херсонская д.43/12, лит. А						
Изм.	Колуч	Лист	№ док	Подпись	Дата	Интерьерные решения Холл-ресепшн			Стадия	Лист	Листов	
Ведущий арх-р	Быков М.М.								Р	1		
Диз-р	Терёхин С.В.											
Диз-р						Ведомость чертежей.			maxdesign			
Н контроль	Быков М.М.											

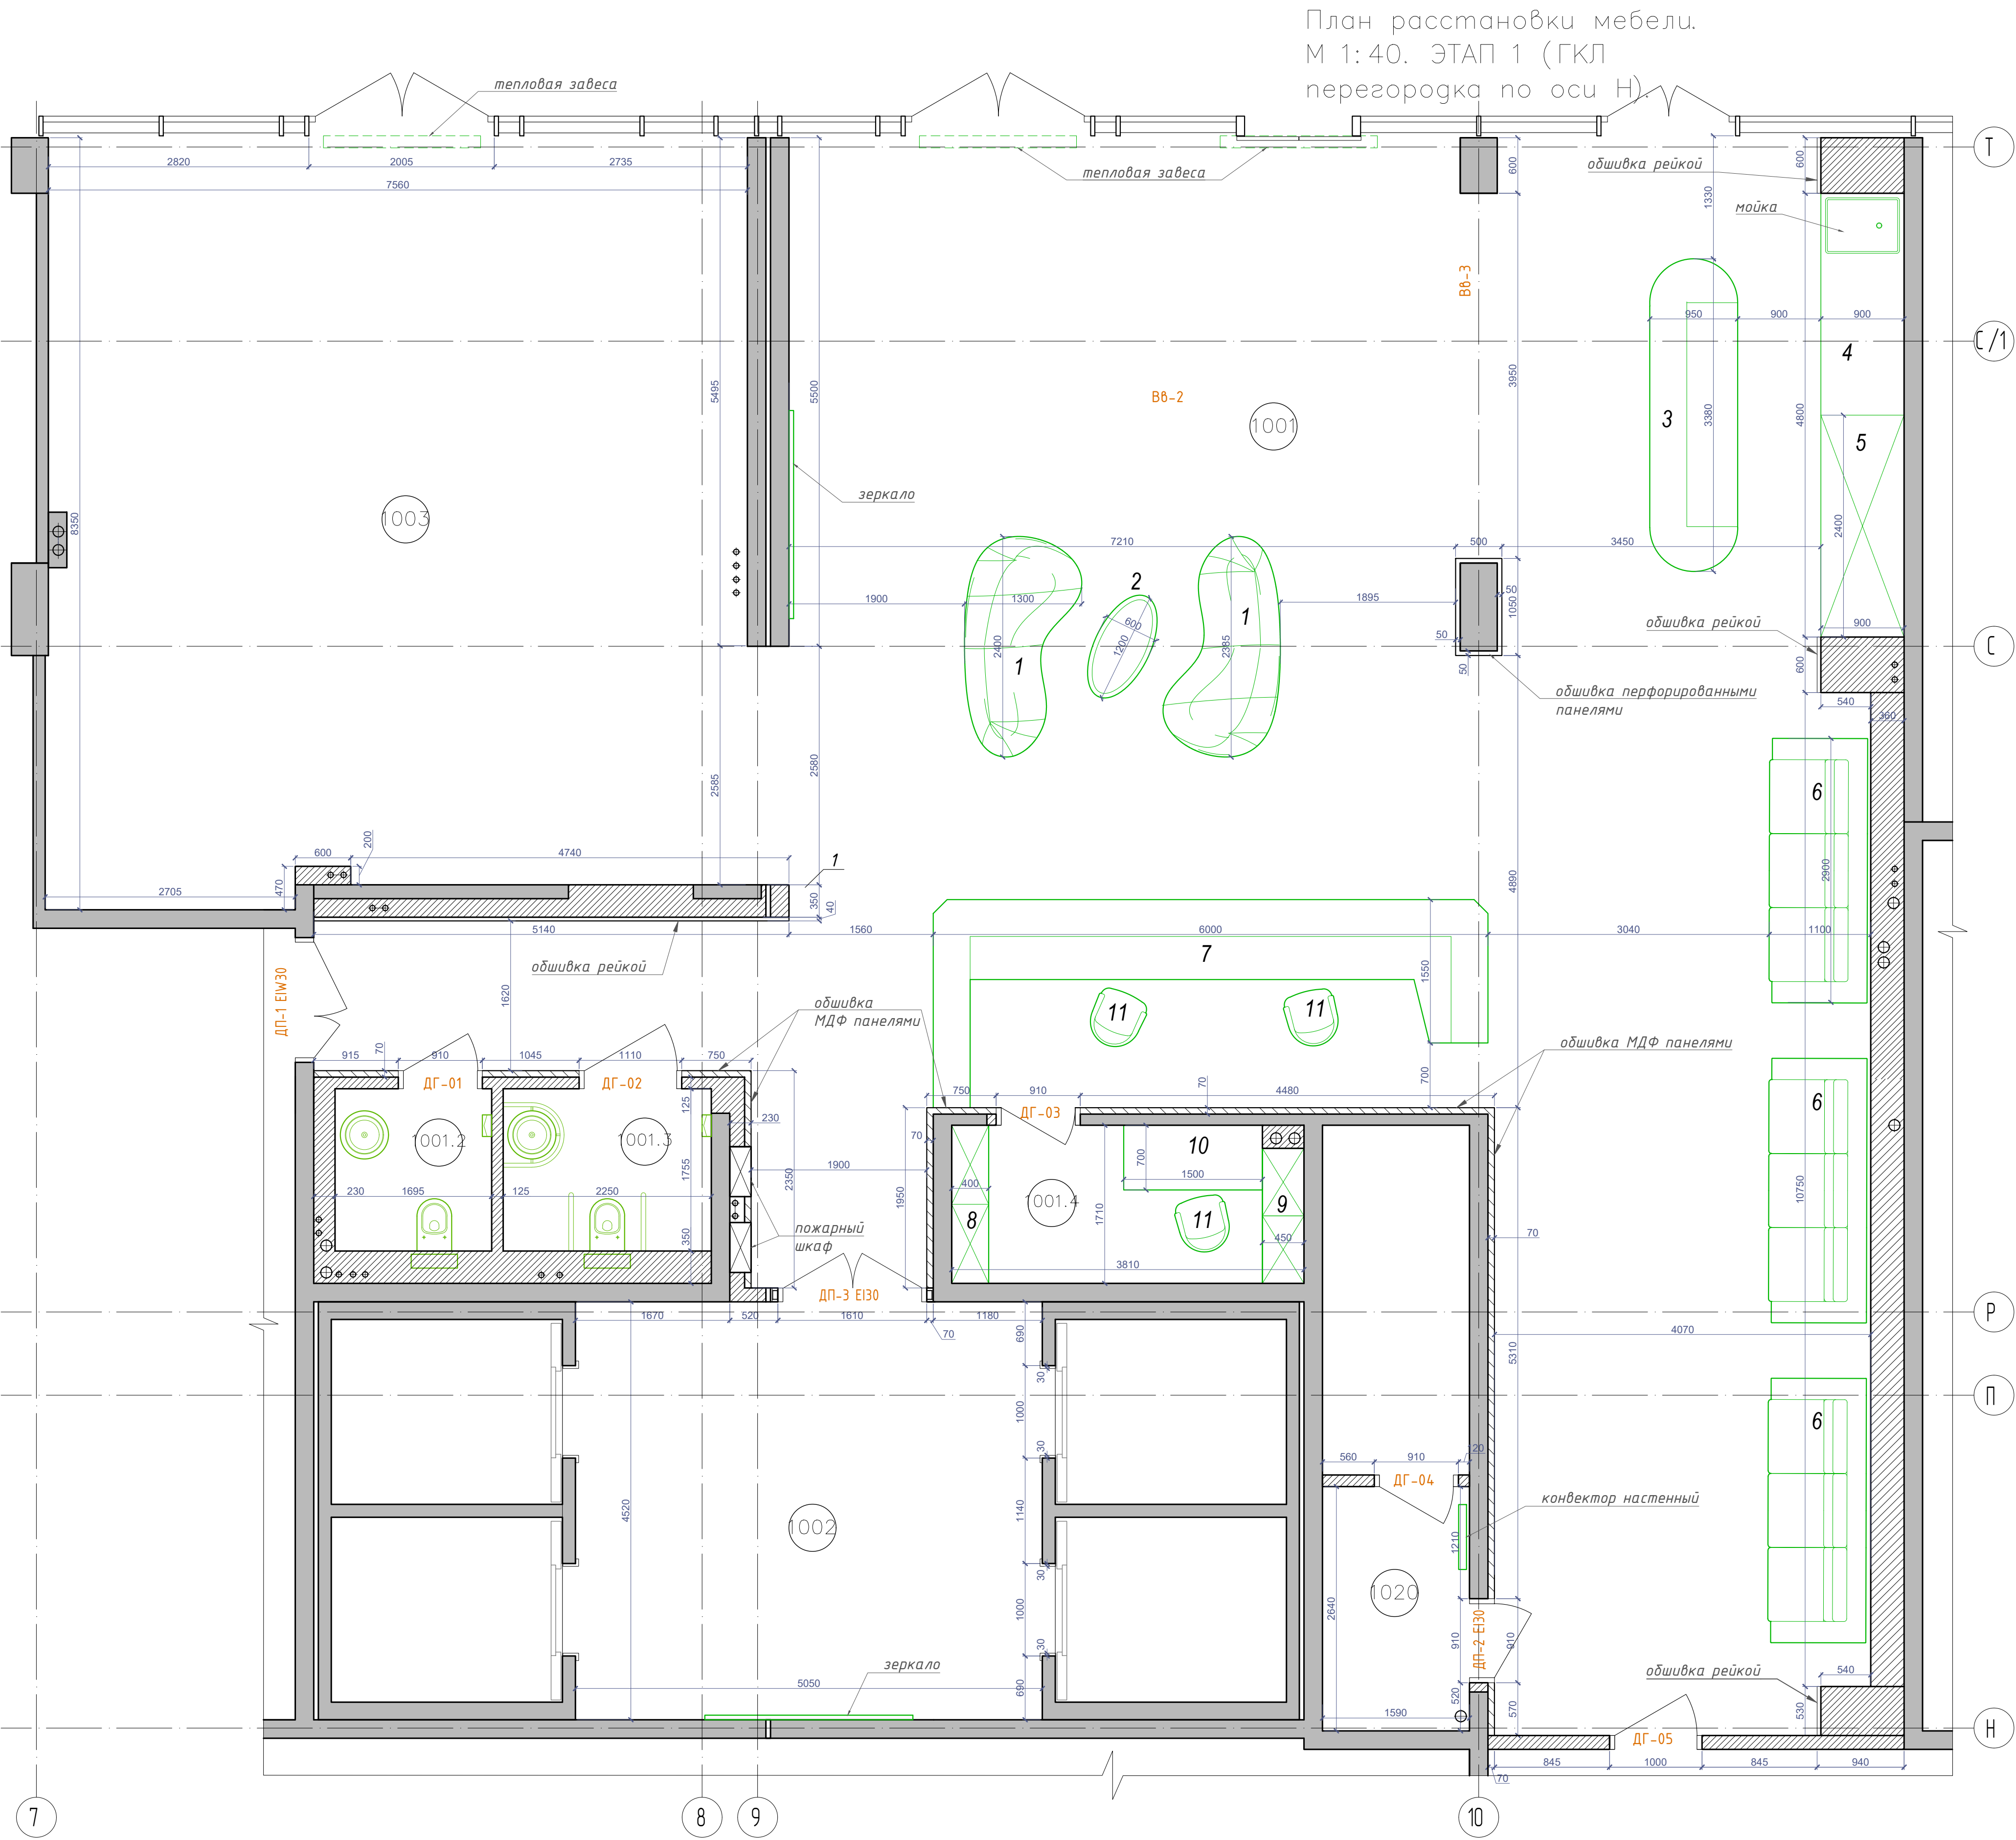

ЭКСПЛИКАЦИЯ ПОМЕЩЕНИЙ:		
№ НА ПЛАНЕ	НАИМЕНОВАНИЕ	ПЛОЩАДЬ, м²
1001	Вестибюль	155,4
1001.2	Санузел	3,1
1001.3	Санузел для МГН	4,2
1001.4	Офис	6,5
1002	Лифтовый холл	22,8
1003	Коммерческое помещение	62,2
1020	Помещение хранения багажа	3,2
Итого:		257 м²

Ведомость мебели		
№ НА ПЛАНЕ	НАИМЕНОВАНИЕ	Кол-во, шт.
1	Диван 2400х1300	2
2	Стол журнальный	1
3	Стойка продавца цветов	1
4	Мебель продавца цветов	1
5	Холодильник для цветов 2400х900	1
6	Диван 2900х1100	3
7	Стойка ресепшен	1
8	Шкаф 1700х400	1
9	Шкаф 1450х450	1
10	Стол 1500х700	1
11	Кресло офисное	3

УСЛОВНЫЕ ОБОЗНАЧЕНИЯ:

② – номер помещения
7 – номер мебели
ДП 01 – обозначение типа двери или витража

ПРИМЕЧАНИЯ:

1. По желанию заказчика перегородка по оси Н с начала возводится из ГКЛ (Этап 1), а затем (Этап 1) производится демонтаж и установка стеклянной перегородки по оси Н.


2. План выполнен по черновым размерам помещений. Требуется корректировка размеров после проведения монтажных работ и чистовой отделки!

3. Мебель на заказ устанавливается фирмой-изготовителем только после дополнительно снятых обмеров специалистами.

4. Сан.тех. оборудование устанавливается в соответствии с тех. картами подключения воды.

5. Выбор и заказ мебели заказчик осуществляет самостоятельно.

				05/2019г.	№ 04.1/АИ-0217
				Объект: апартаменты. Адрес: г. Санкт-Петербург, ул. Херсонская д.43/12, лит. А	
Изм.	Копия	Лист	№ дж	Подпись	Дата
Ведущий арх-р	Быков М.М.				
Диз-р	Терехин С.В.				
Диз-р					
				Интерьерные решения Холл-ресепшн	Стадия
				Р	Лист
				2	Листов
				План расстановки мебели. ЭТАП 1 (ГКЛ перегородка по оси Н).	maxdesign
Н контроль	Быков М.М.				

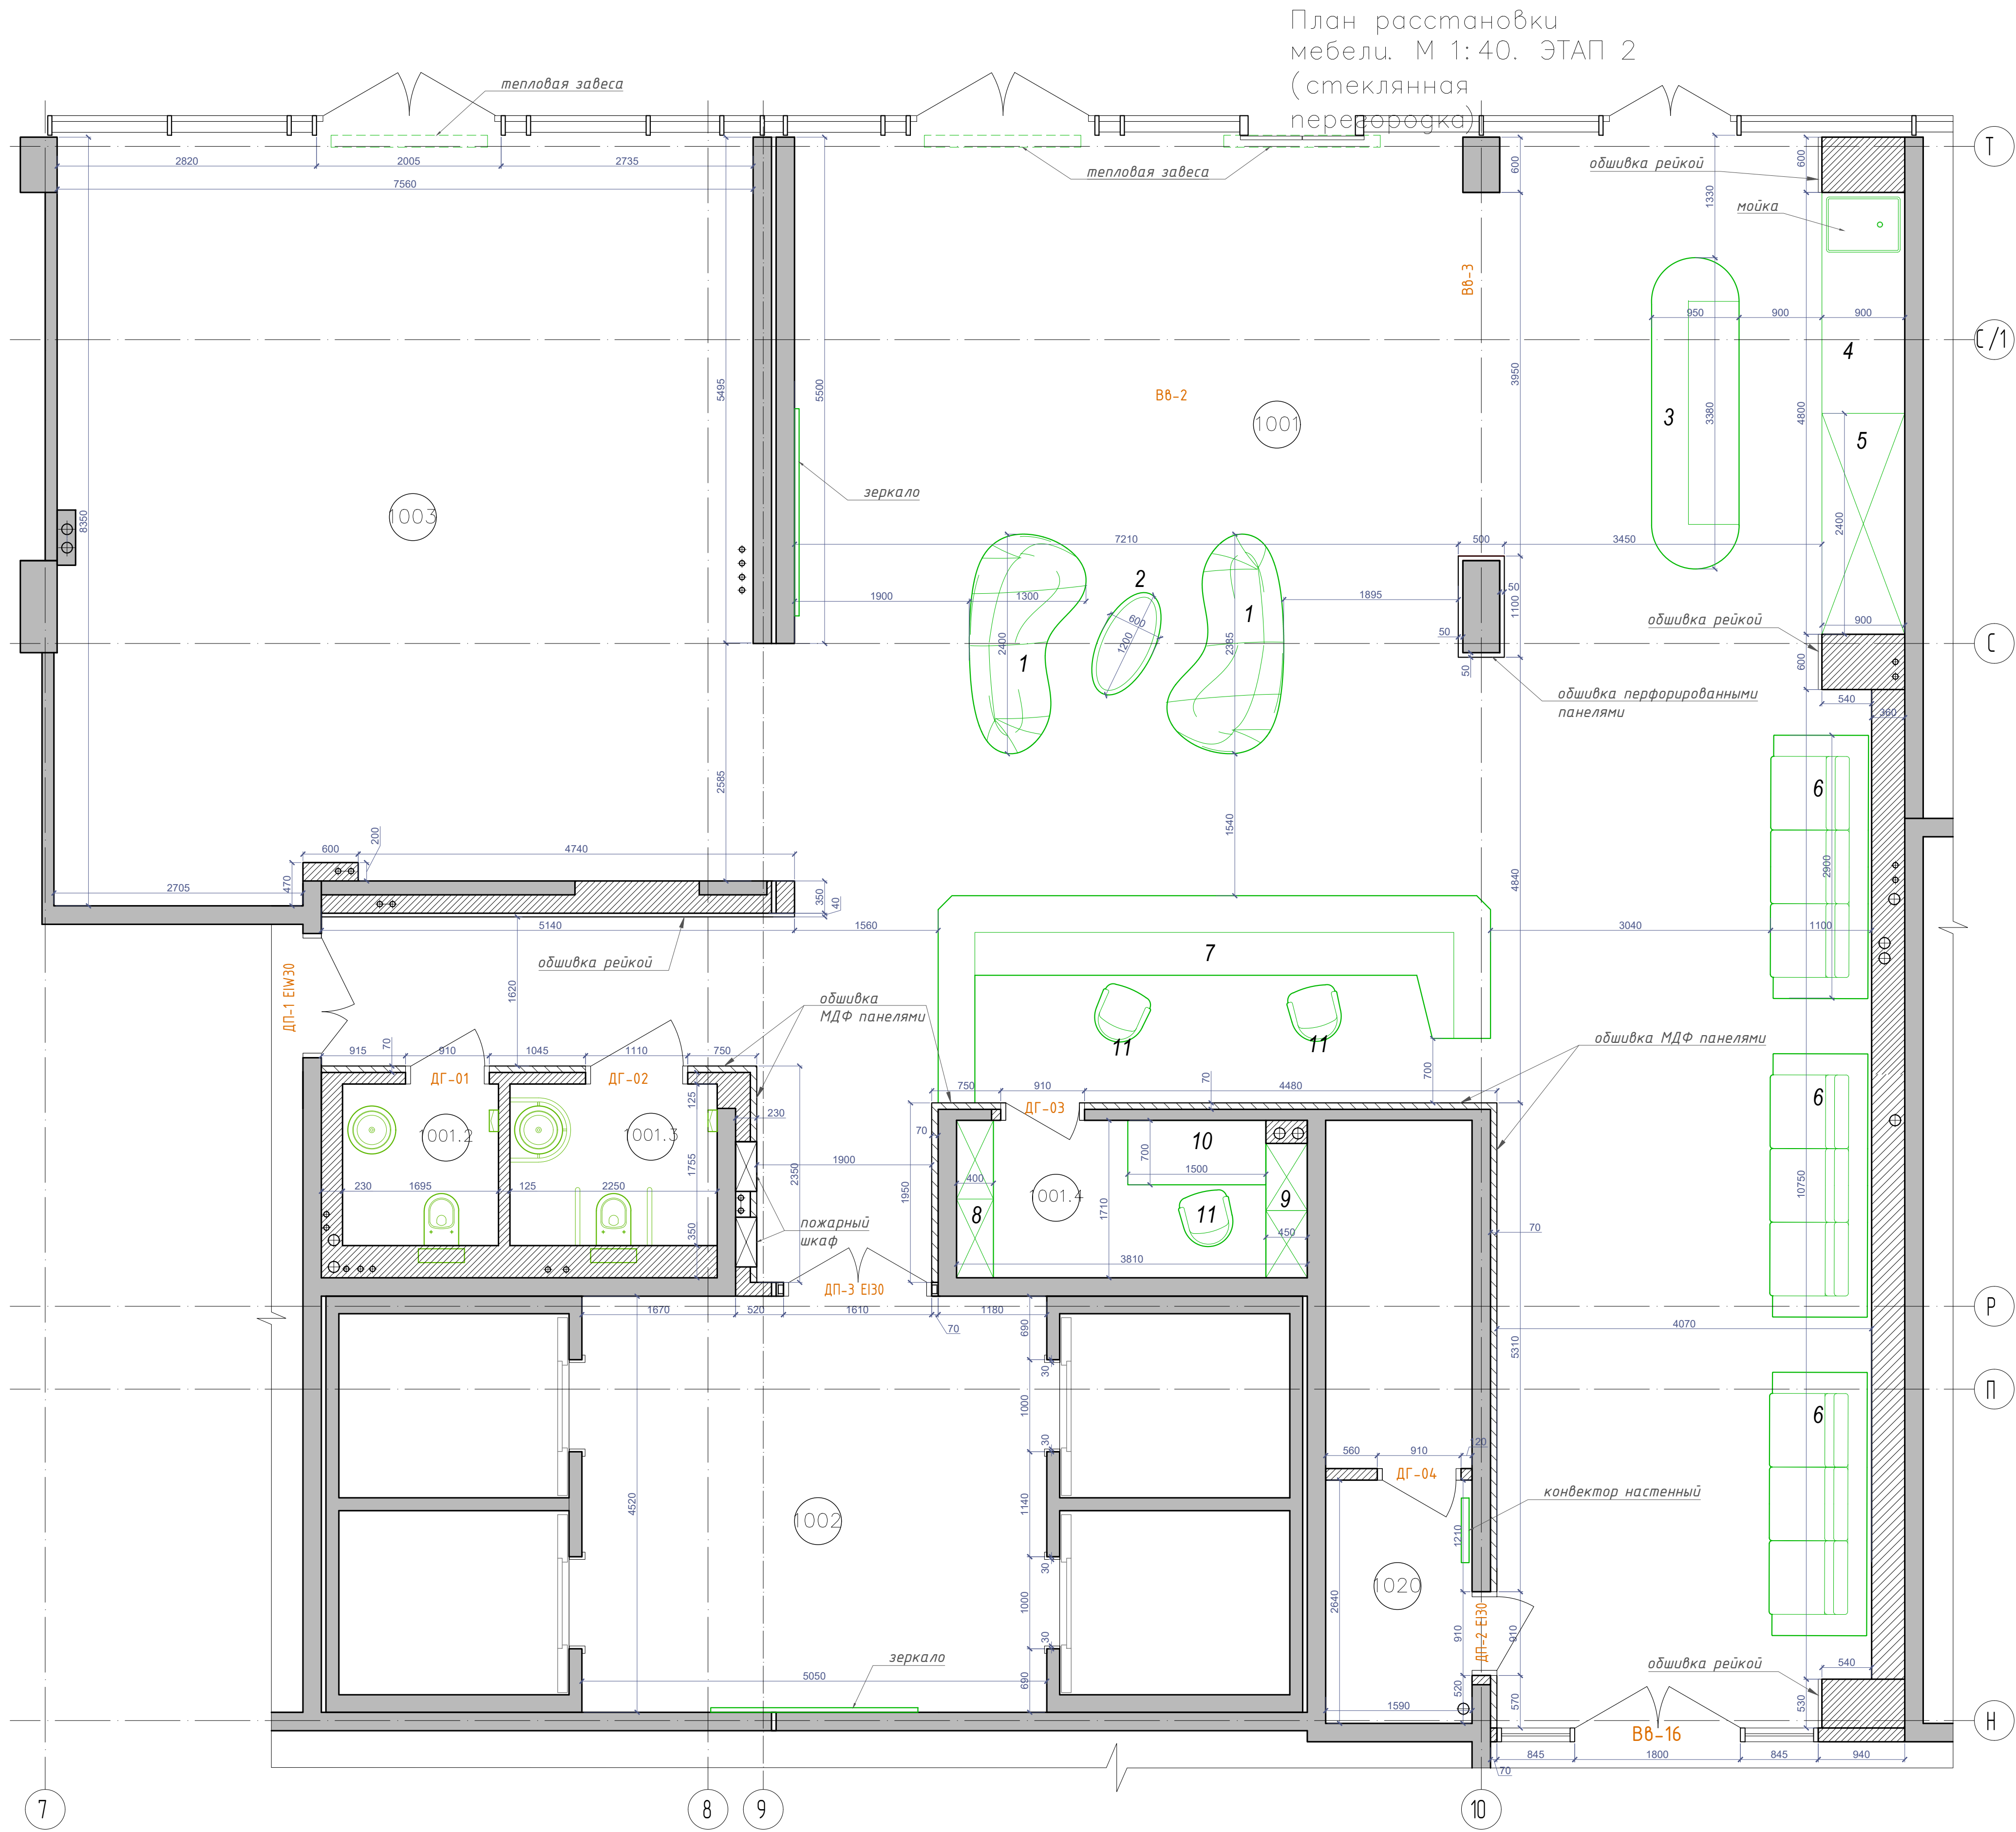

ЭКСПЛИКАЦИЯ ПОМЕЩЕНИЙ:

№ НА ПЛАН Е	НАИМЕНОВАНИЕ	ПЛОЩАДЬ, м²
1001	Вестибюль	155,4
1001.2	Санузел	3,1
1001.3	Санузел для МГН	4,2
1001.4	Офис	6,5
1002	Лифтовый холл	22,8
1003	Коммерческое помещение	62,2
1020	Помещение хранения багажа	3,2
Итого:		257 м²

Ведомость мебели

№ НА ПЛАН Е	НАИМЕНОВАНИЕ	Кол-во, шт.
1	Диван 2400х1300	2
2	Стол журнальный	1
3	Стойка продавца цветов	1
4	Мебель продавца цветов	1
5	Холодильник для цветов 2400х900	1
6	Диван 2900х1100	3
7	Стойка ресепшен	1
8	Шкаф 1700х400	1
9	Шкаф 1450х450	1
10	Стол 1500х700	1
11	Кресло офисное	3

УСЛОВНЫЕ ОБОЗНАЧЕНИЯ:


- ② – номер помещения
7 – номер мебели
ДП 01 – обозначение типа двери или витража

ПРИМЕЧАНИЯ:

1. По желанию заказчика перегородка по оси Н с начала возводится из ГКЛ (Этап 1), а затем (Этап 1) производится демонтаж и установка стеклянной перегородки.
2. План выполнен по черновым размерам помещений. Требуется корректировка размеров после проведения монтажных работ и чистовой отделки!
3. Мебель на заказ устанавливается фирмой-изготовителем только после дополнительно снятых обмеров специалистами.
4. Сан.тех. оборудование устанавливается в соответствии с тех. картами подключения воды.
5. Выбор и заказ мебели заказчик осуществляет самостоятельно.

					05/2019г.	№ 04.1/ АИ-0217			
						Объект: апартамент-отель. Адрес: г. Санкт-Петербург, ул. Херсонская д.43/12, лит. А			
Изм.	Копия	Лист	№ док	Подпись	Дата	Интерьерные решения Холл-ресепшн	Стадия	Лист	Листов
Ведущий арх-р			Быков М.М.				Р	3	
Диз-р			Терехин С.В.						
Диз-р						План расстановки мебели. М 1:40. ЭТАП 2 (стеклянная перегородка)	maxdesign		
Н. контроль			Быков М.М.						

План демонтажа стен и переноса коммуникаций. М 1:50

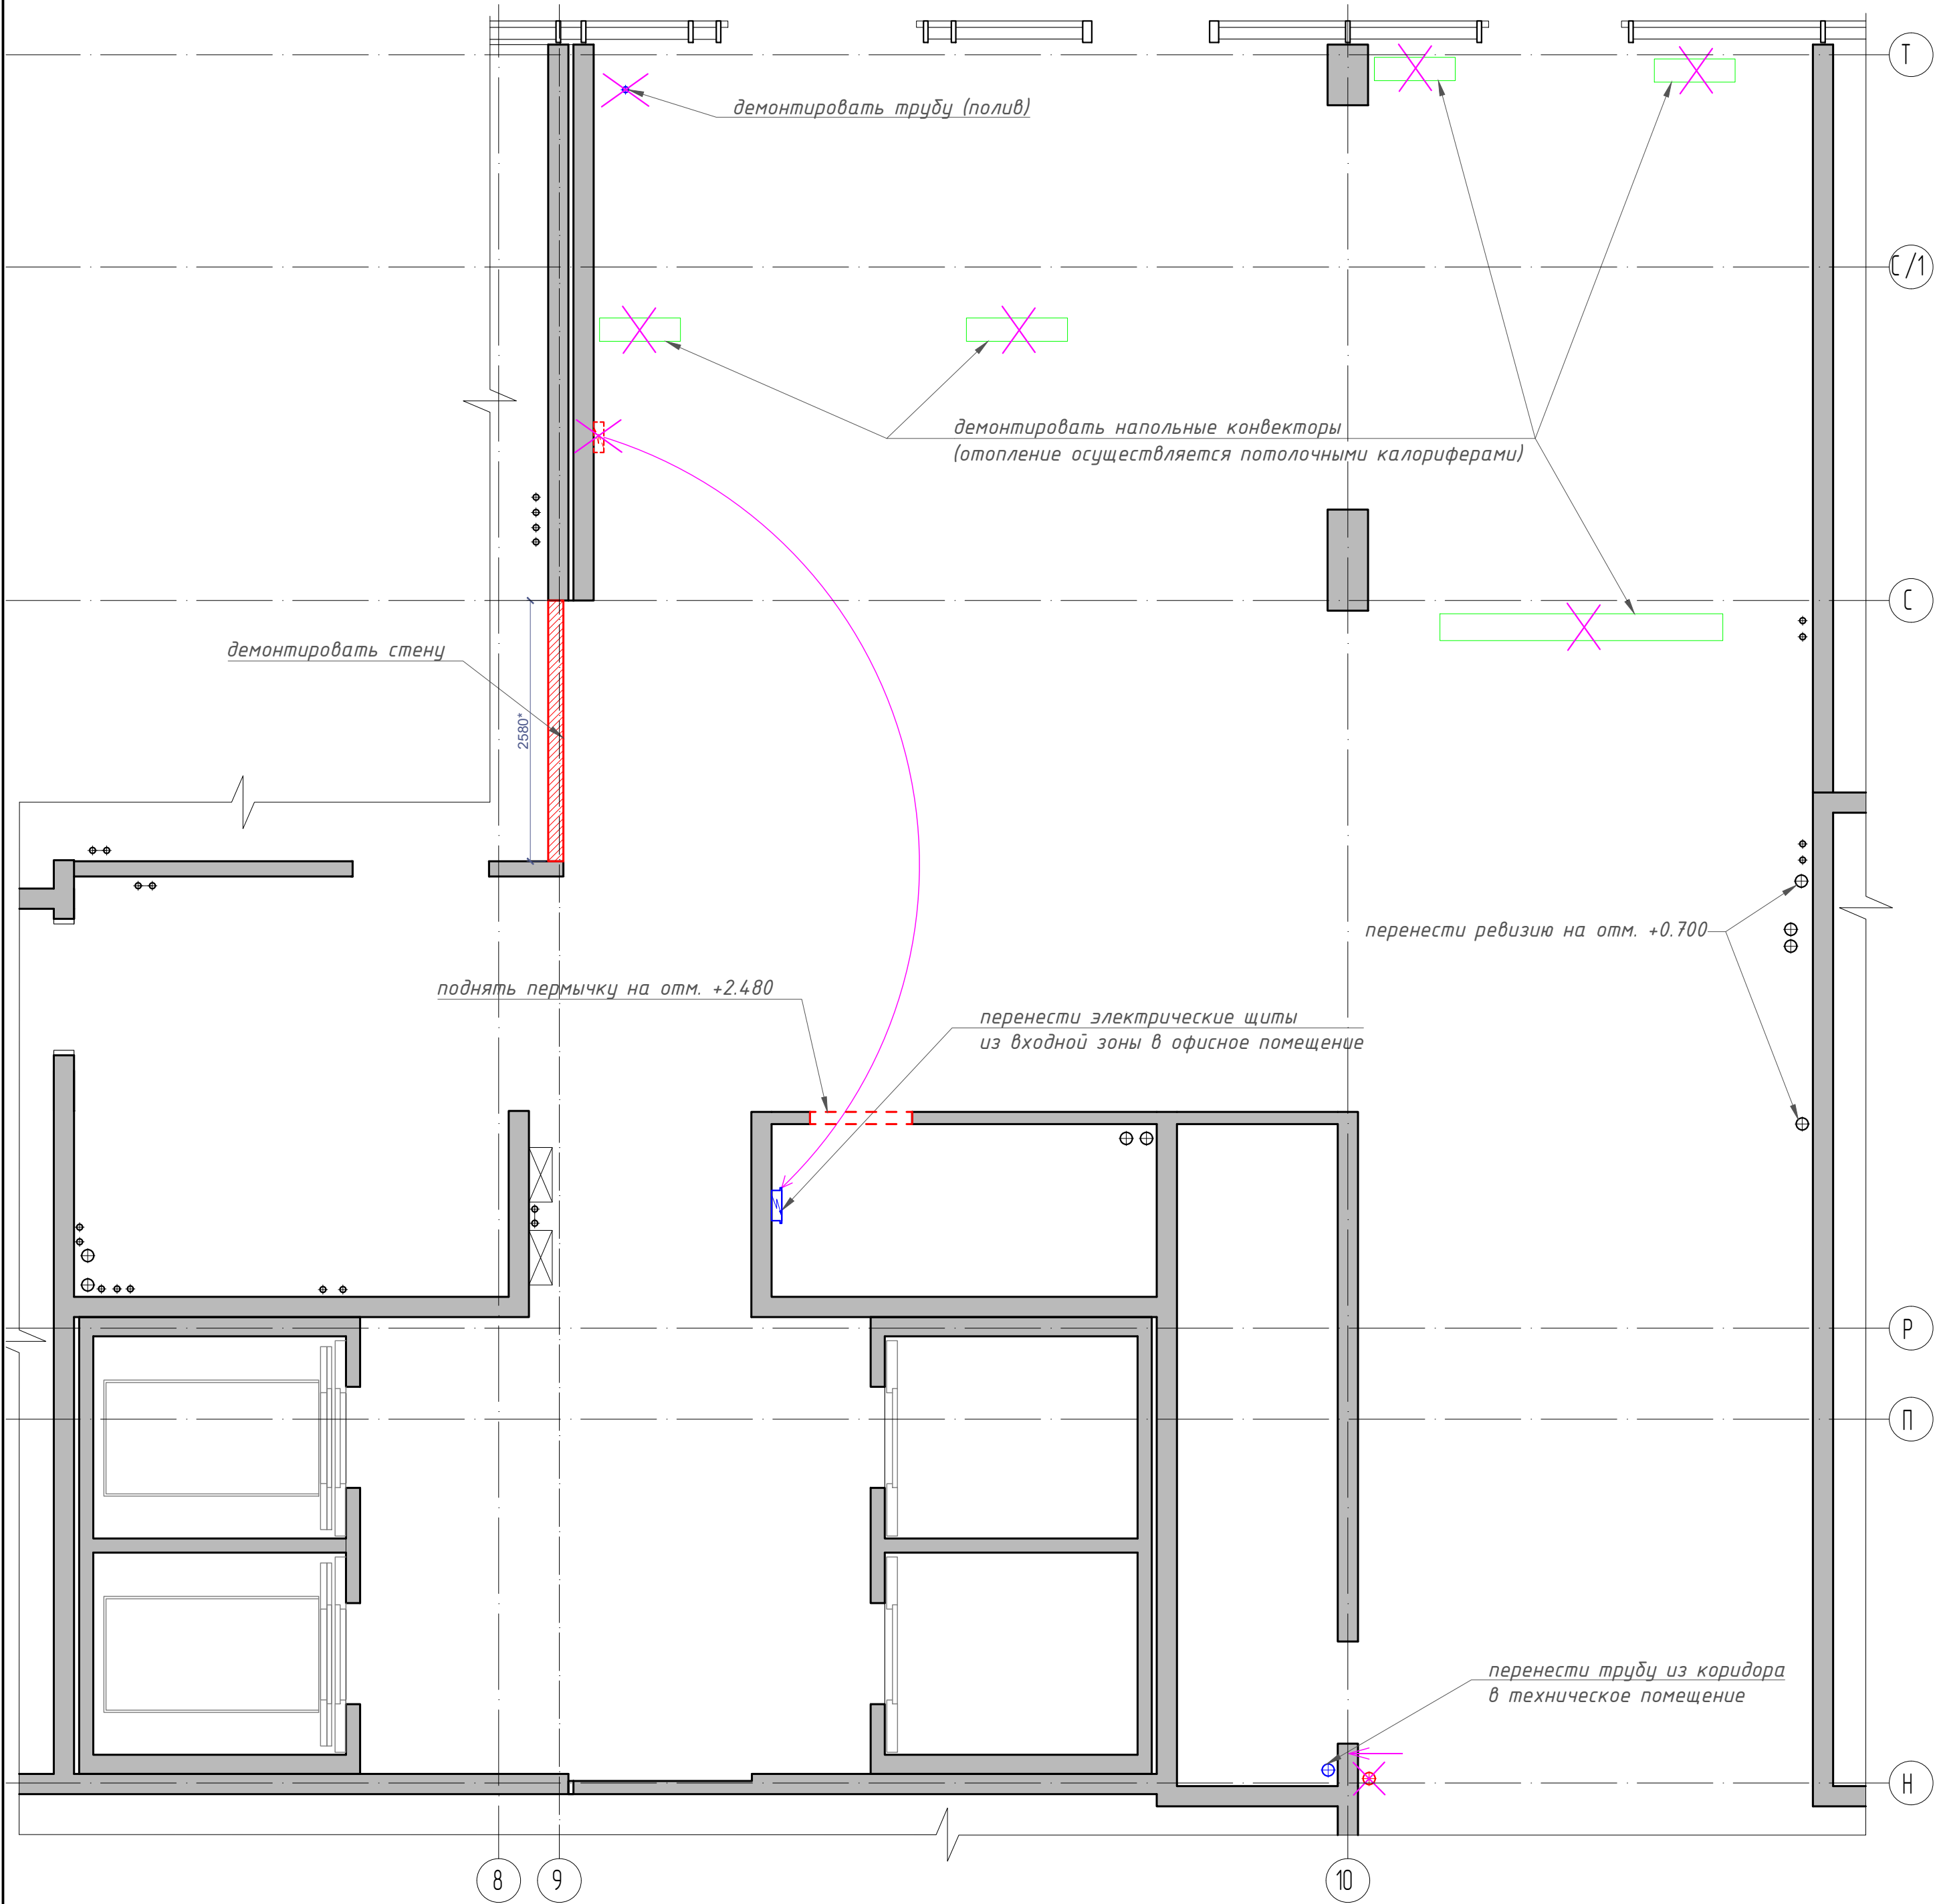


УСЛОВНЫЕ ОБОЗНАЧЕНИЯ:

- демонтируемые стены
- демонтируемые коммуникации
- новое положение коммуникаций
- направление переноса коммуникаций

- ПРИМЕЧАНИЯ:
- 1. * - размеры для справок.
 - 2. Отметки от уровня чистого пола 1-го этажа


						05/2019г.			№ 041/АИ-0217			
						Объект: апарт-отель. Адрес: г. Санкт-Петербург, ул. Херсонская д.43/12, лит. А						
Изм.	Колуч	Лист	№ док	Подпись	Дата	Интерьерные решения Холл-ресепшн			Стадия	Лист	Листов	
Ведущий арх-р	Быков М.М.								Р	4		
Диз-р	Терёхин С.В.											
Диз-р						План демонтажа стен и переноса коммуникаций.			maxdesign			
Н контроль	Быков М.М.											

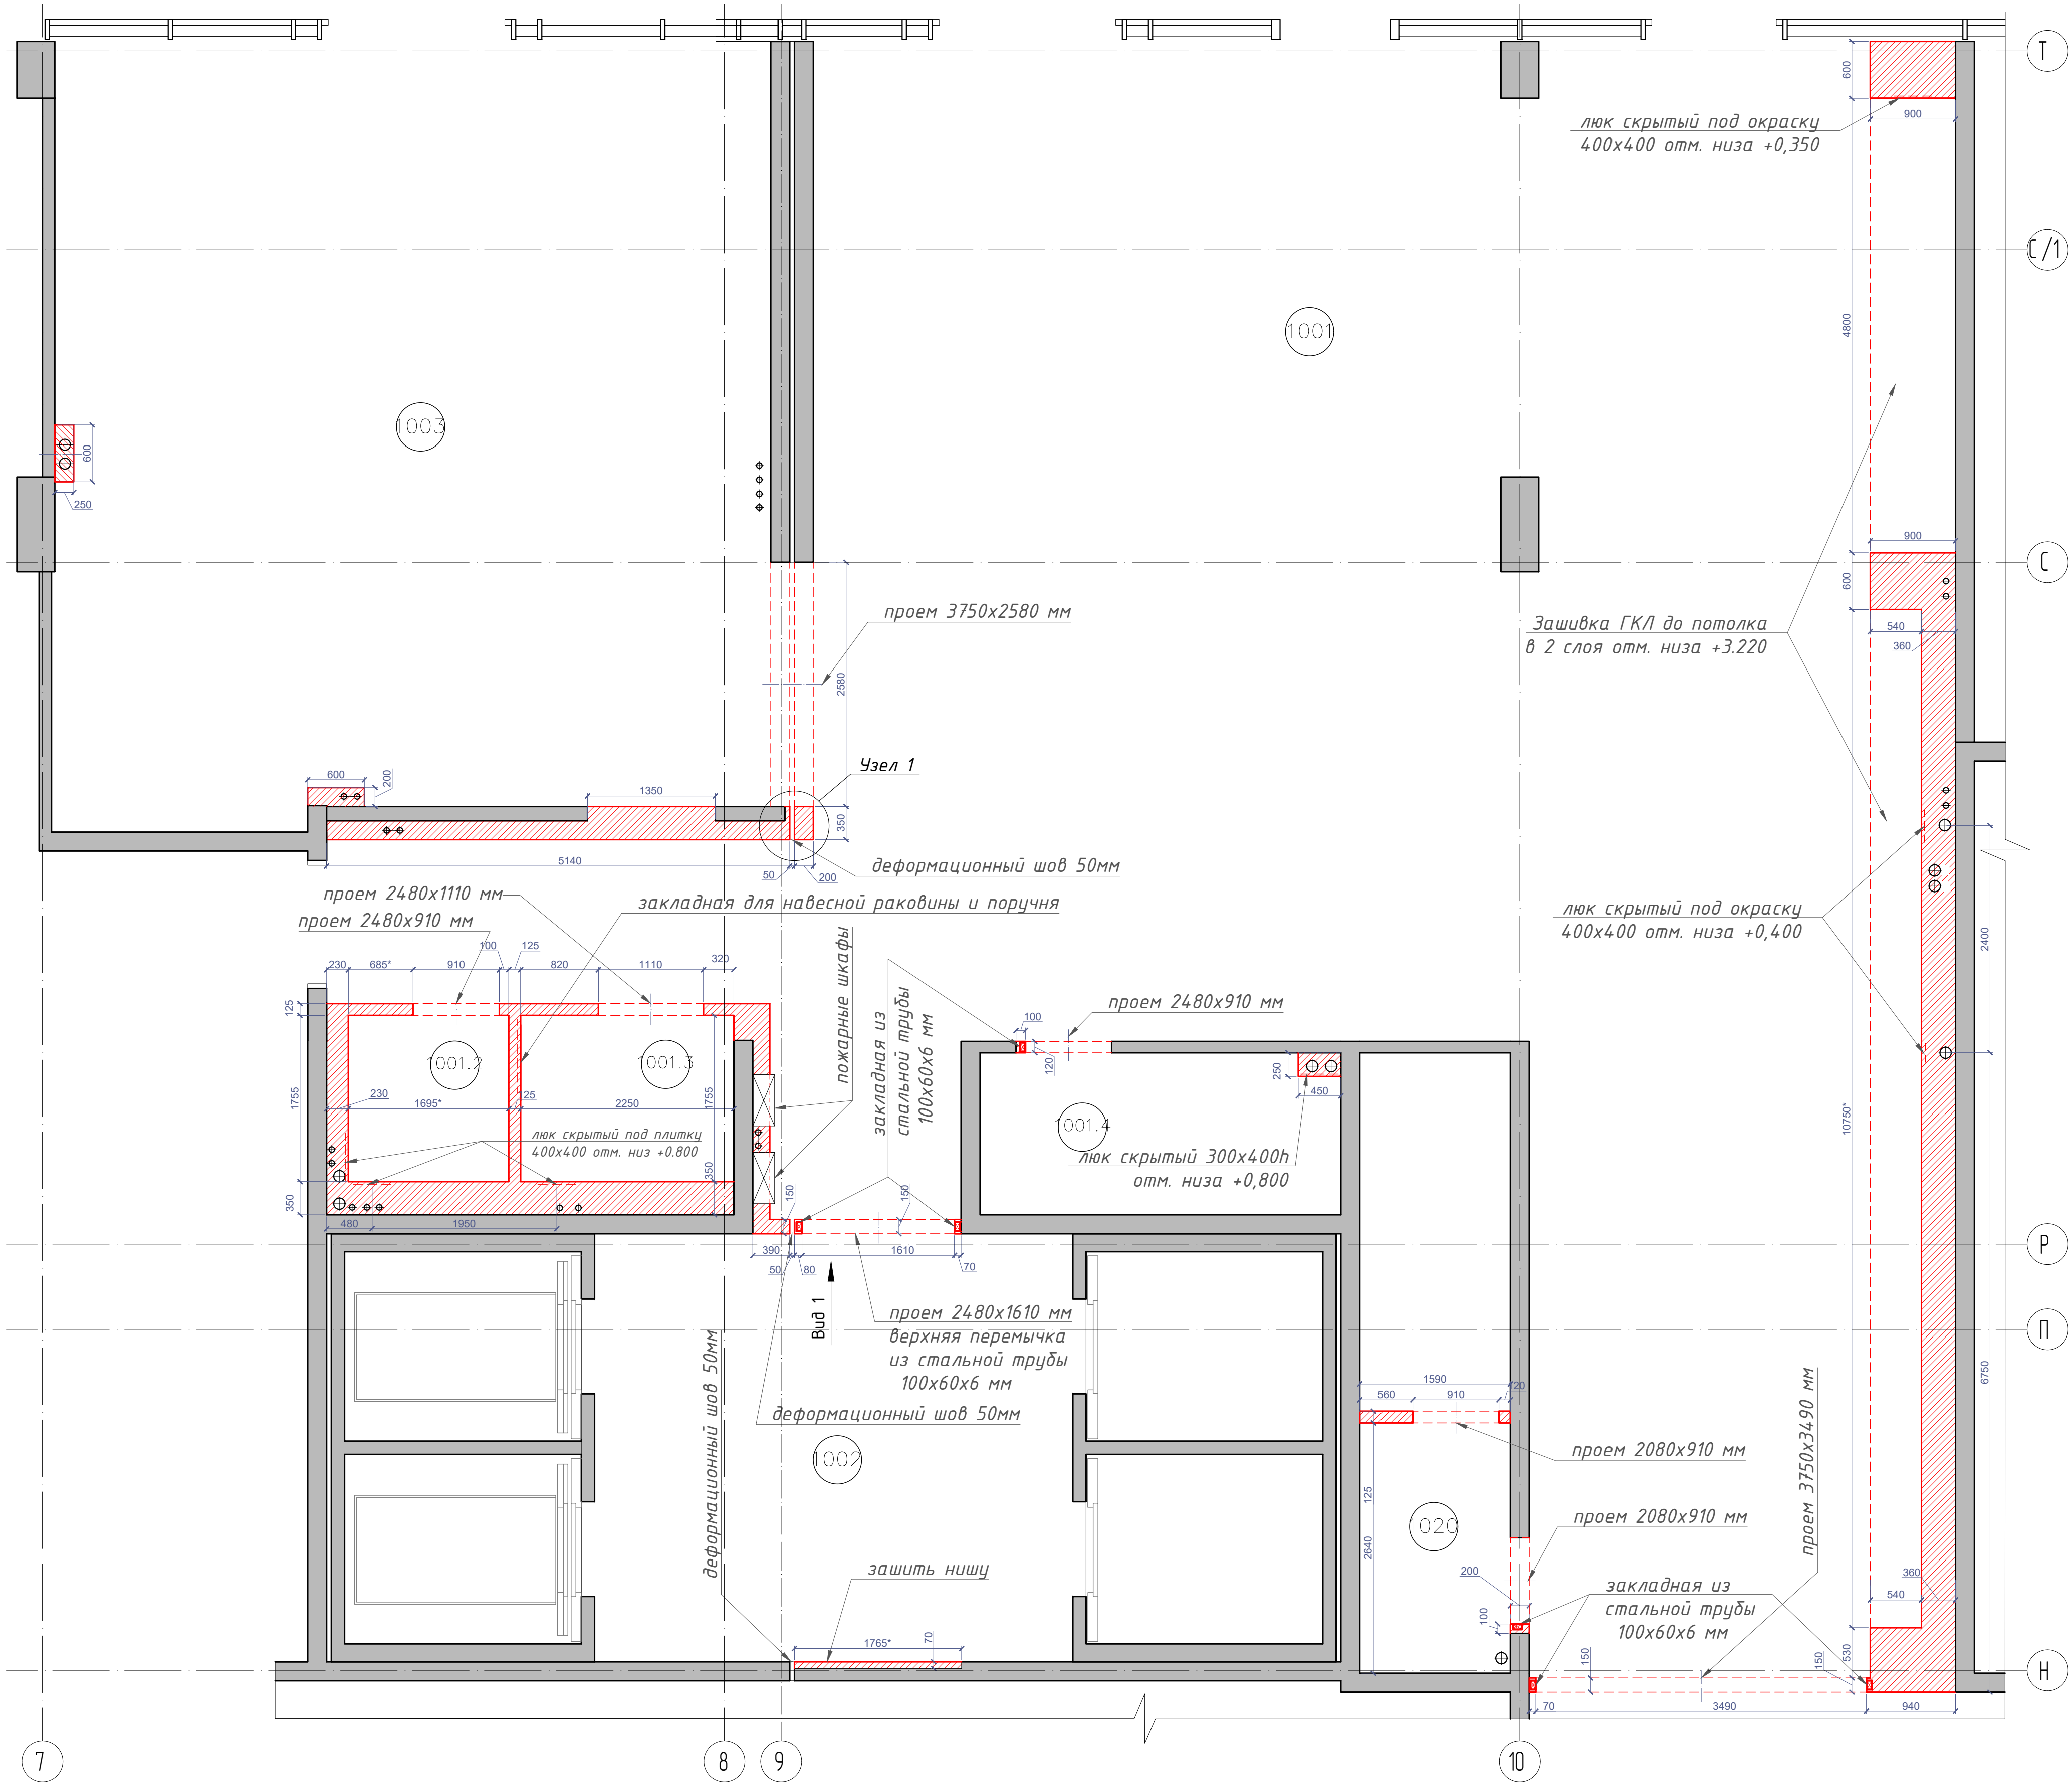

ЭКСПЛИКАЦИЯ ПОМЕЩЕНИЙ:

№ НА ПЛАНЕ	НАИМЕНОВАНИЕ	ПЛОЩАДЬ, м²
1001	Вестибюль	155,4
1001.2	Санузел	3,1
1001.3	Санузел для МГН	4,2
1001.4	Офис	6,5
1002	Лифтовый холл	22,8
1003	Коммерческое помещение	62,2
1020	Помещение хранения багажа	3,2
Итого:		257 м²

УЗЕЛ 1

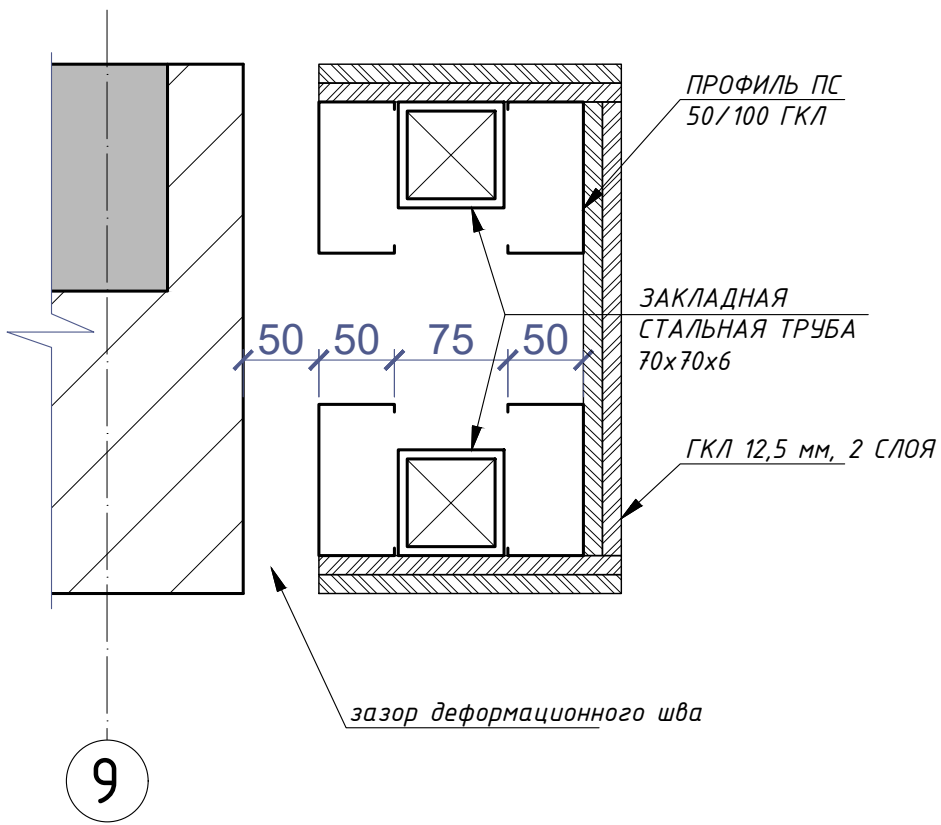


УСЛОВНЫЕ ОБОЗНАЧЕНИЯ:

— возводимые конструкции ГКЛ
площадь ГКЛ конструкций = 240м²

- ПРИМЕЧАНИЯ:
- * - размеры для справок.
 - Допускается изменение размера и положения ревизионных люков по согласованию с дизайнером осуществляющим авторский надзор.
 - Конструкции ГКЛ выполнять в соответствии с типовыми решениями KNAUF. Тип перегородок KNAUF C112. Тип обшивки стен KNAUF C623.
 - Вид 1 см. на листе 5 "Схема перегородки в лифтовый холл".
 - Данный лист смотреть совместно с листом 5 "Схема перегородки в лифтовый холл".
 - Обшивку влажных помещений выполнить из влагостойкого гипсокартона.
 - Данный лист смотреть совместно с развертками помещений настоящего проекта

						05/2019г.			№ 04.1/ АИ-0217					
						Объект: апартамент-отель. Адрес: г. Санкт-Петербург, ул. Херсонская д.43/12, лит. А								
Изм.	Копия	Лист	№ док.	Подпись	Дата	Интерьерные решения Холл-ресепшн			Стадия	Лист	Листов			
Ведущий арх-р			Быков М.М.						Р	5				
Диз-р			Терехин С.В.											
Диз-р						План возведения перегородок			maxdesign					
Н.Контроль			Быков М.М.											


СХЕМА ПЕРЕГОРОДКИ В ЛИФТОВЫЙ ХОЛЛ (М1:20)

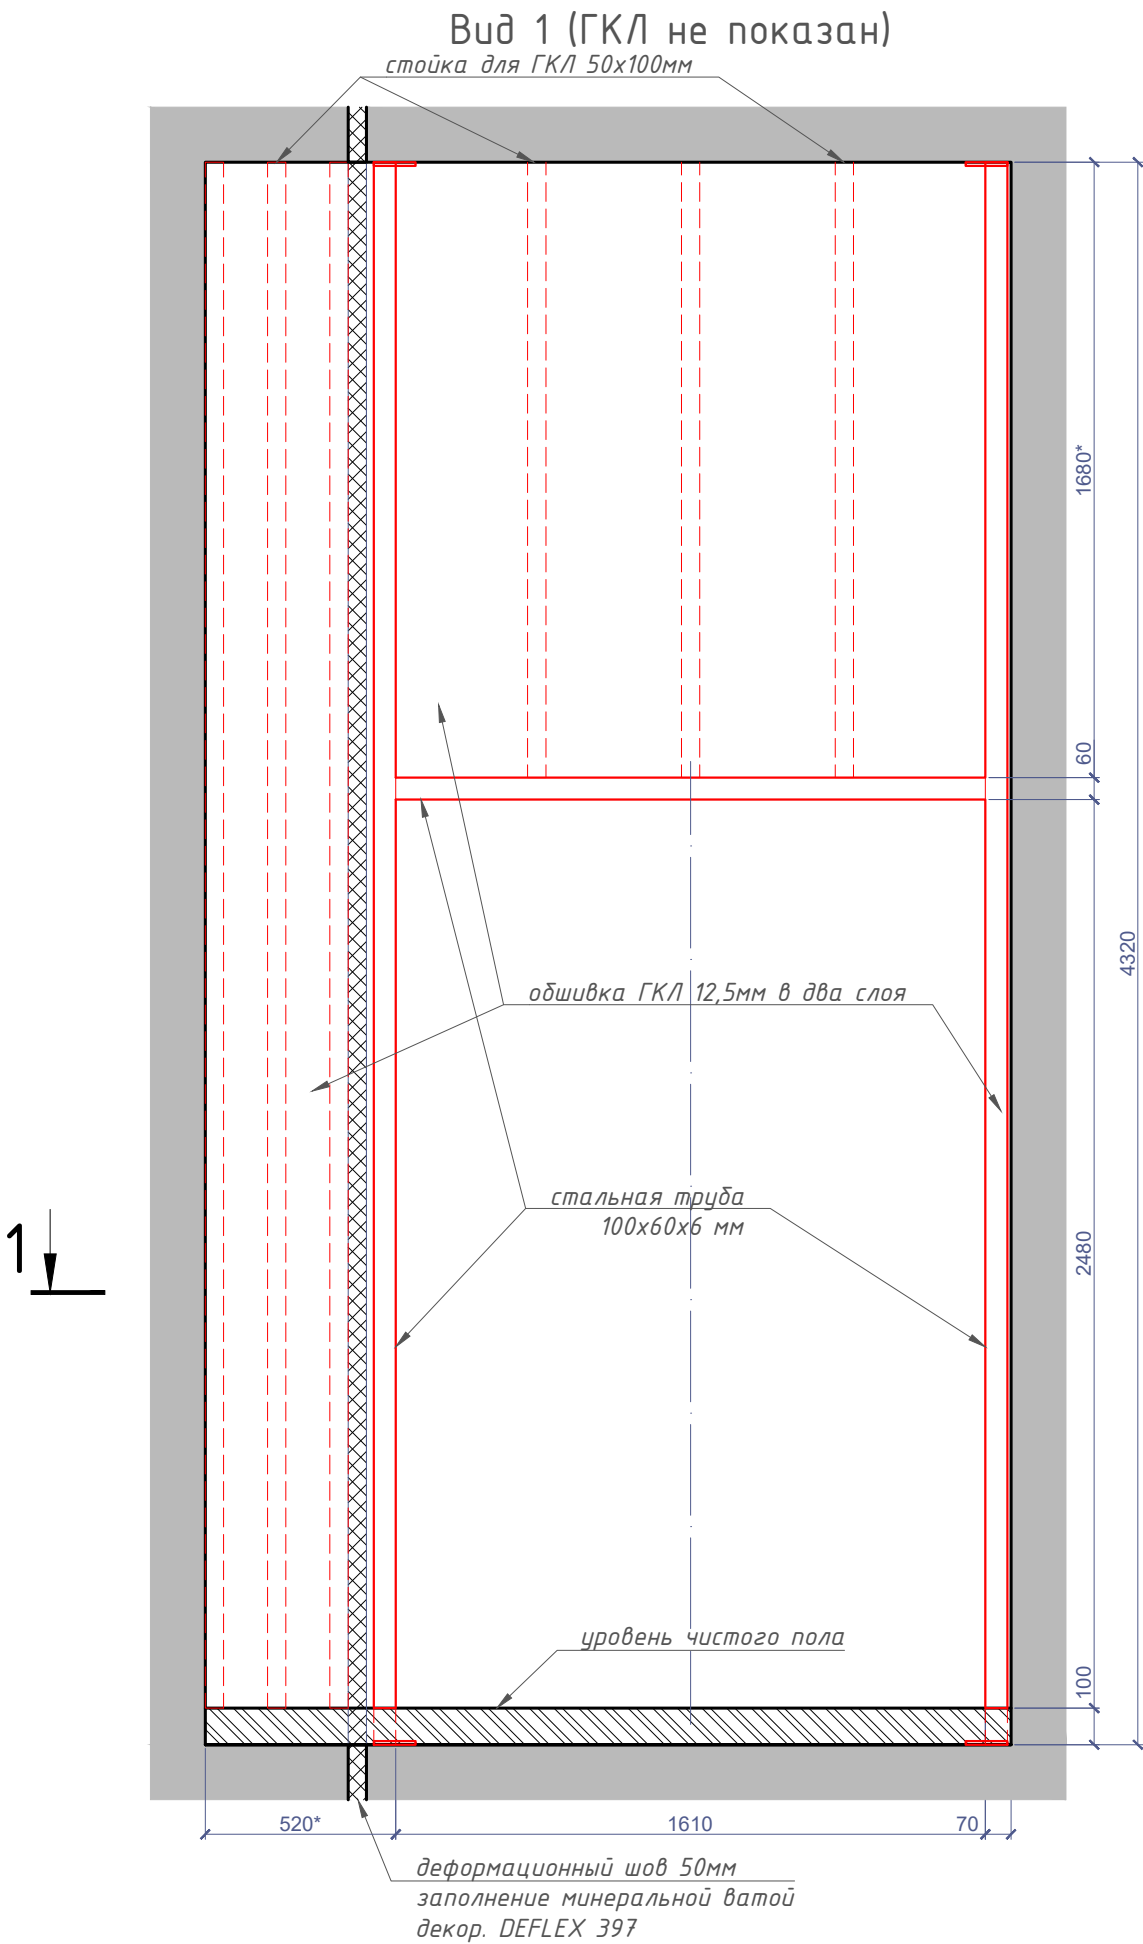


Узел 1 (М1:10)



Указатель вуга

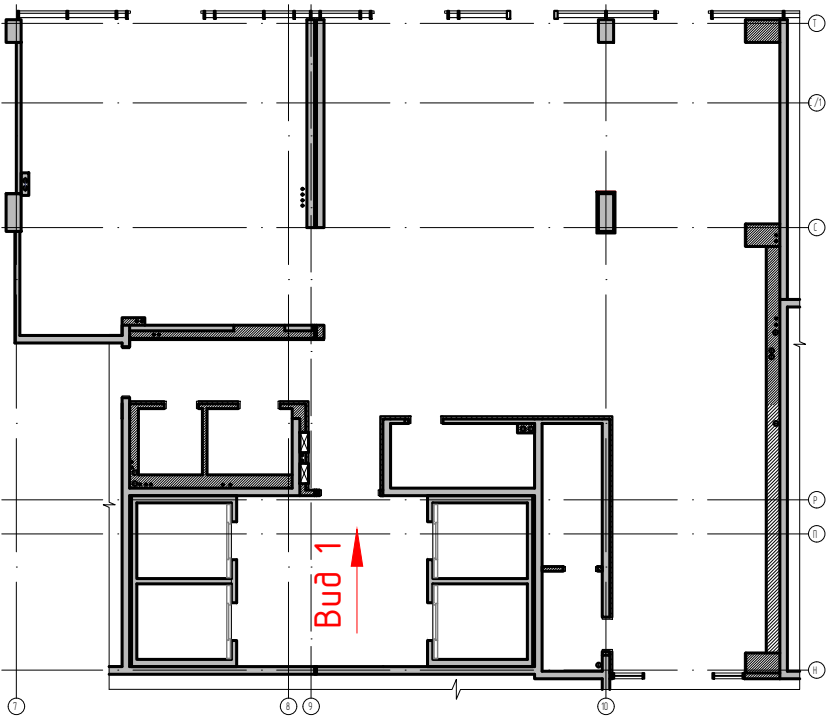

Разрез 1-1

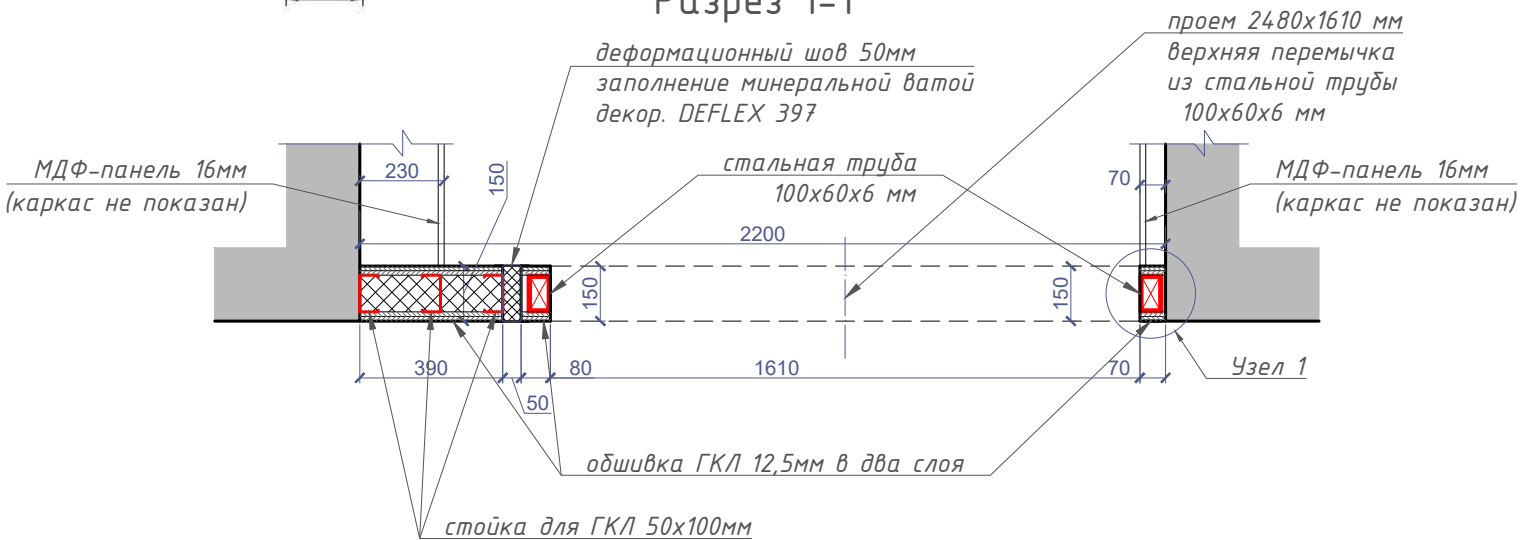


ПРИМЕЧАНИЯ:

- * - размеры для справок.
- Конструкции ГКЛ выполнить в соответствии с типовыми решениями KNAUF.
Тип перегородок KNAUF C112 (обшивка ГКЛ 12,5мм в два слоя с двух сторон).
- Данный лист смотреть совместно с листом 4 "План возведения перегородок и монтажа".
- Приведенные размеры указываются от предчистовой отделки

						05/2019г.			№041/АИ-0217			
						Объект: апарт-отель. Адрес: г. Санкт-Петербург, ул. Херсонская д.43/12, лит. А						
Изм.	Колуч.	Лист	№ док.	Подпись	Дата	Интерьерные решения Холл-ресепшн	Стадия	Лист	Листов			
Ведущий арх-р	Быков М.М.						Р	6				
Диз-р	Терёхин С.В.											
Диз-р						Схема перегородки в лифтовый холл.	maxdesign					
Н. контроль.	Быков М.М.											

План размещения сантехнических приборов. М 1:50

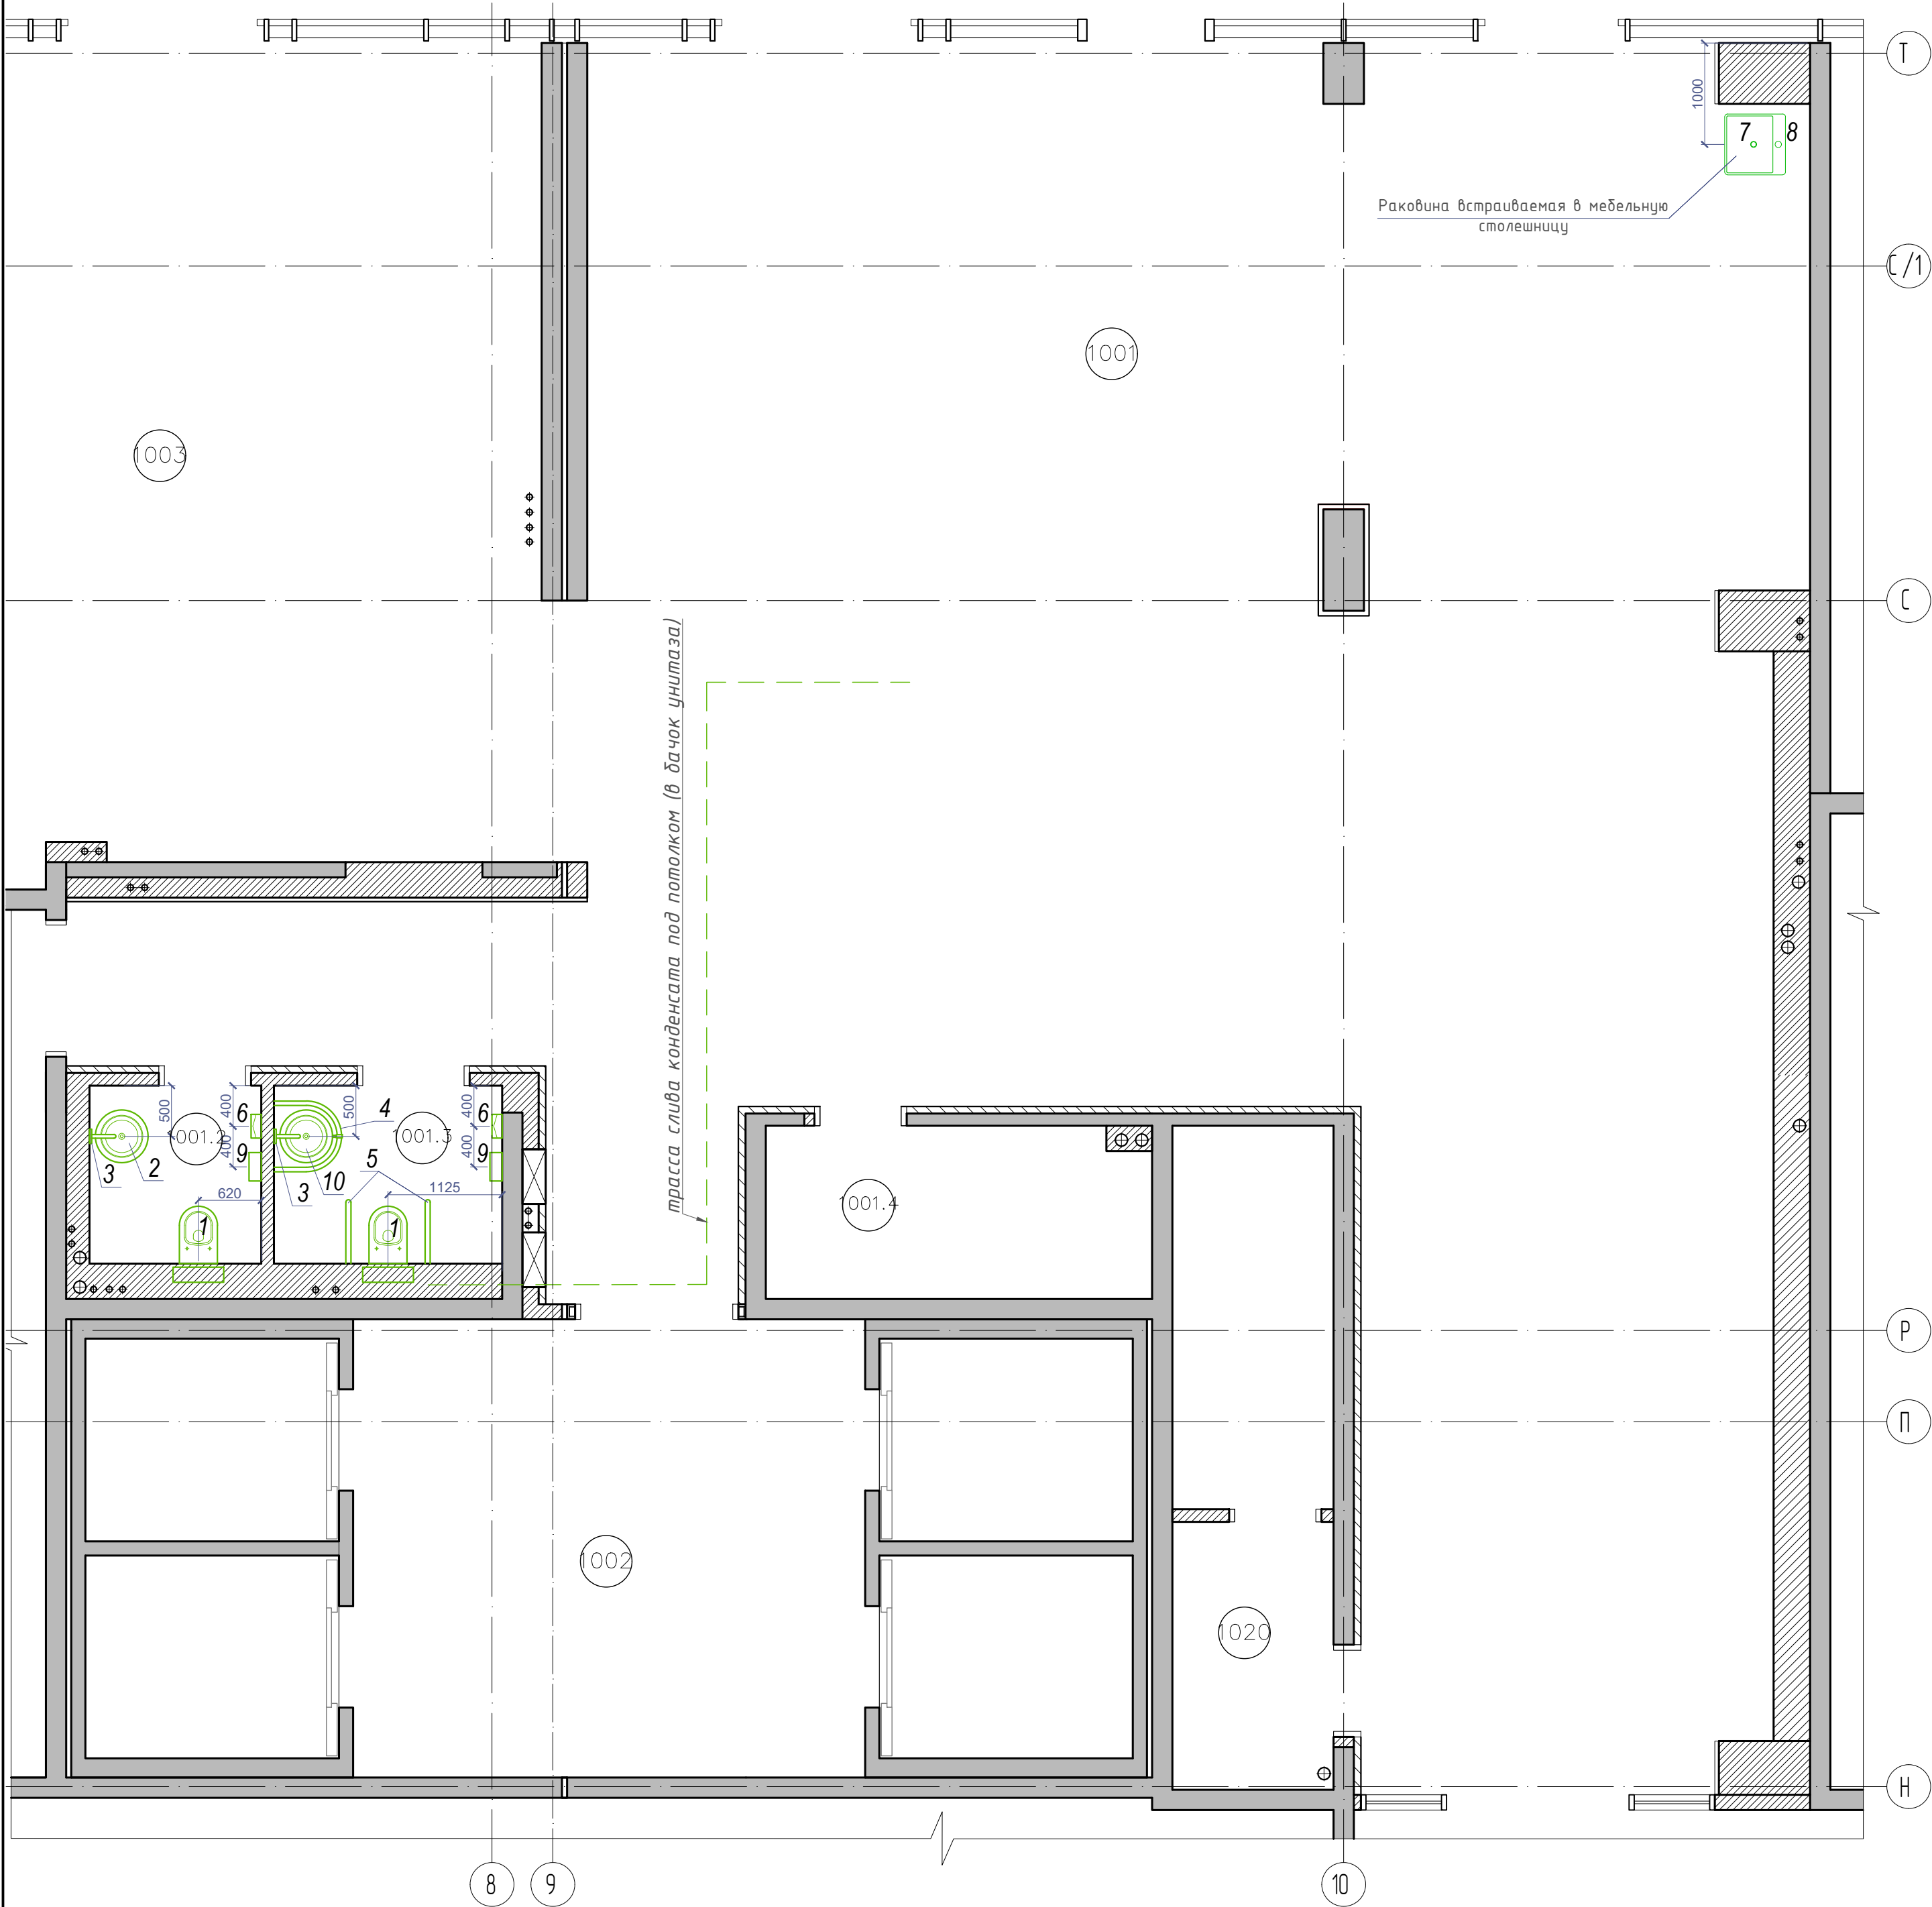

ЭКСПЛИКАЦИЯ ПОМЕЩЕНИЙ:

№ НА ПЛАНЕ	НАИМЕНОВАНИЕ	ПЛОЩАДЬ, м²
1001	Вестибюль	155,4
1001.2	Санузел	3,1
1001.3	Санузел для МГН	4,2
1001.4	Офис	6,5
1002	Лифтовый холл	22,8
1003	Коммерческое помещение	62,2
1020	Помещение хранения багажа	3,2

Итого: 257 м²

ПЕРЕЧЕНЬ ОБОРУДОВАНИЯ

№ НА ПЛАНЕ	НАИМЕНОВАНИЕ	Кол-во, шт.
1	Унитаз подвесной с инсталляцией	2
2	Раковина круглая - тумба	1
3	Смеситель для раковины из стены, бесконтактный	2
4	Поручень раковины для инвалидов	1
5	Поручень унитаза для инвалидов	1 компл.
6	Сушилка для рук Dyson Airblade V HU02 Nickel	2
7	Раковина встраиваемая в мебельную столешницу	1
8	Смеситель для встроенной раковины	1
9	Диспенсер туалетной бумаги	2
10	Раковина круглая подвесная для инвалидов	1

УСЛОВНЫЕ ОБОЗНАЧЕНИЯ:

- ② - номер помещения
7 - номер оборудования

ПРИМЕЧАНИЯ:

1. * - размеры для справок.
2. Данный лист см. совместно листами разверток стен.
3. Выбор сантехнического оборудования осуществляется заказчиком или его представителем самостоятельно.

						05/2019г.				№ 041/ АИ-0217				
						Объект: апарт-отель. Адрес: г. Санкт-Петербург, ул. Херсонская д.43/12, лит. А								
Изм.	Колуч	Лист	№ док	Подпись	Дата	Интерьерные решения Холл-ресепшн			Стадия	Лист	Листов			
Ведущий арх-р		Быков М.М.							Р	7				
Диз-р		Терехин С.В.												
Диз-р						План размещения сантехнических приборов.			maxdesign					
Н. контроль		Быков М.М.												




УСЛОВНЫЕ ОБОЗНАЧЕНИЯ

обознач.	Наименование	Кол-во
②	Номер помещения	
---	Плинтус керамогрант пиленный, h100мм, цвет антрацит	75 м.п.
---	Плинтусный кабель-канал. Hager SL 20X55 мм С КОМПЕНСАЦИЕЙ НЕРОВНОСТЕЙ СТЕН, ЦВЕТ ЧЕРНЫЙ RAL9011	22 м.п.
---	Деформационный шов Deflex 446/b-050 h=15мм, накладка серого цвета.	11,5 м.п.
+	Керамогранит MILLENNIUM SILVER NAT RET 800X1600, 9мм	234 м2
□	Керамогранит 600х600 светлый, гр. износ. не менее PEI IV, коэф. скольжения не менее R11	8 м2
—	Керамогранит Италон Surface Корпен, нарезка 800х90	87 шт.
—	Латунь листовая 800х90	100 шт.
—	Грязезащитное покрытие Emco diplomat 522G, 22мм	6,5 м2
0.000	Отметка чистого пола.	
↔	Начало и направление раскладки	


ПРИМЕЧАНИЯ:

- Площади покрытий даны чистые (без учета запаса).
- Верх напольного покрытия на проектной отметке чистого пола, если не указано иное.
- Уточнить размеры после завершения штукатурных работ.
- Для монтажа грязезащитного покрытия выполнить углубления 20мм.
- За отм. 0.000 принята отметка чистого пола первого этаж.
- Стыковку разнородных материалов в области дверных проемов осуществлять по середине дверного полотна.
- При монтаже деформационного шва соблюдать рекомендации завода – изготовителя.


Узел 1. Устройства деформационного шва. М 1:5 (принципиальная схема)

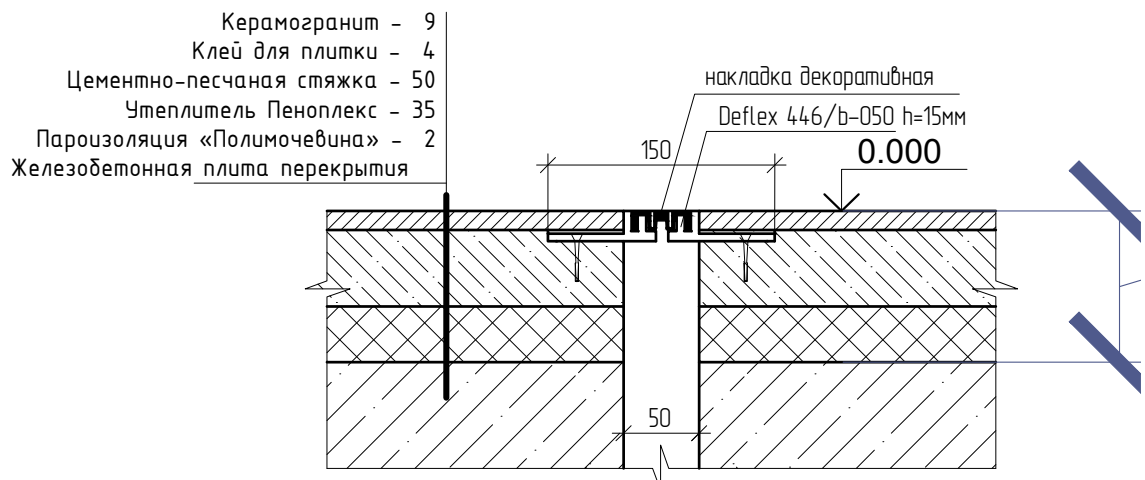

Узел 2. Углубления для грязезащитного покрытия. М 1:5

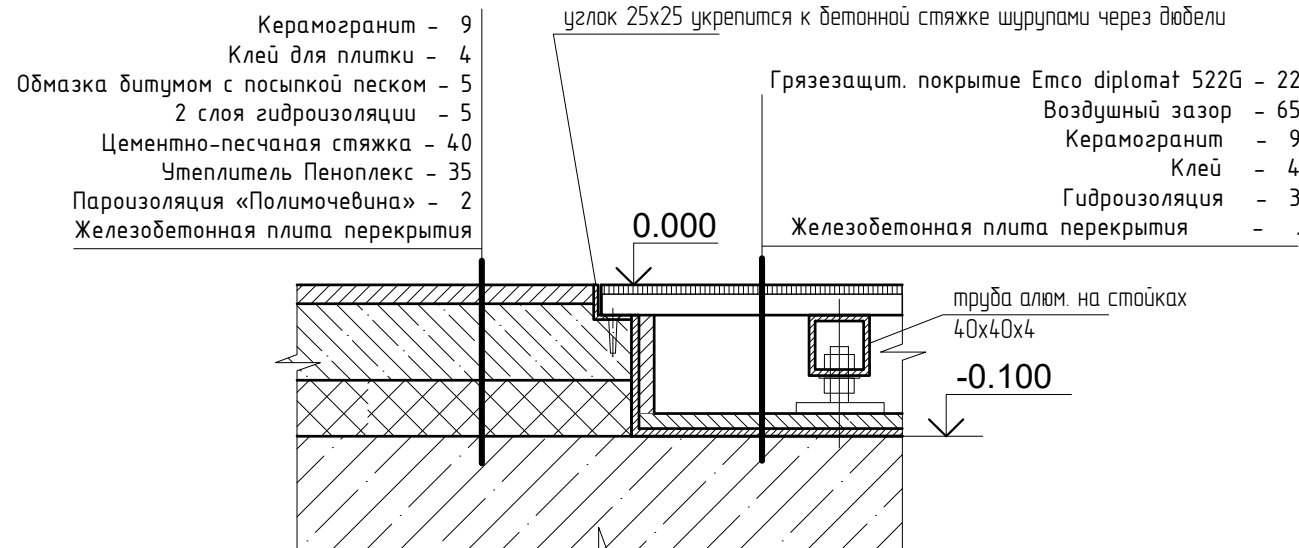

					05/2019г.	№ 04.1/АИ-0217
					Объект: апартаменты.	
					Адрес: г. Санкт-Петербург, ул. Херсонская д.43/12, лит. А	
Изм.	Кол-во	Лист	№ док.	Подпись	Дата	Стация
Ведущий арх-р	1	8	1	Быков М.М.		Р
Диз-р	1			Терехин С.В.		
Диз-р	1					
И контроль	1			Быков М.М.		

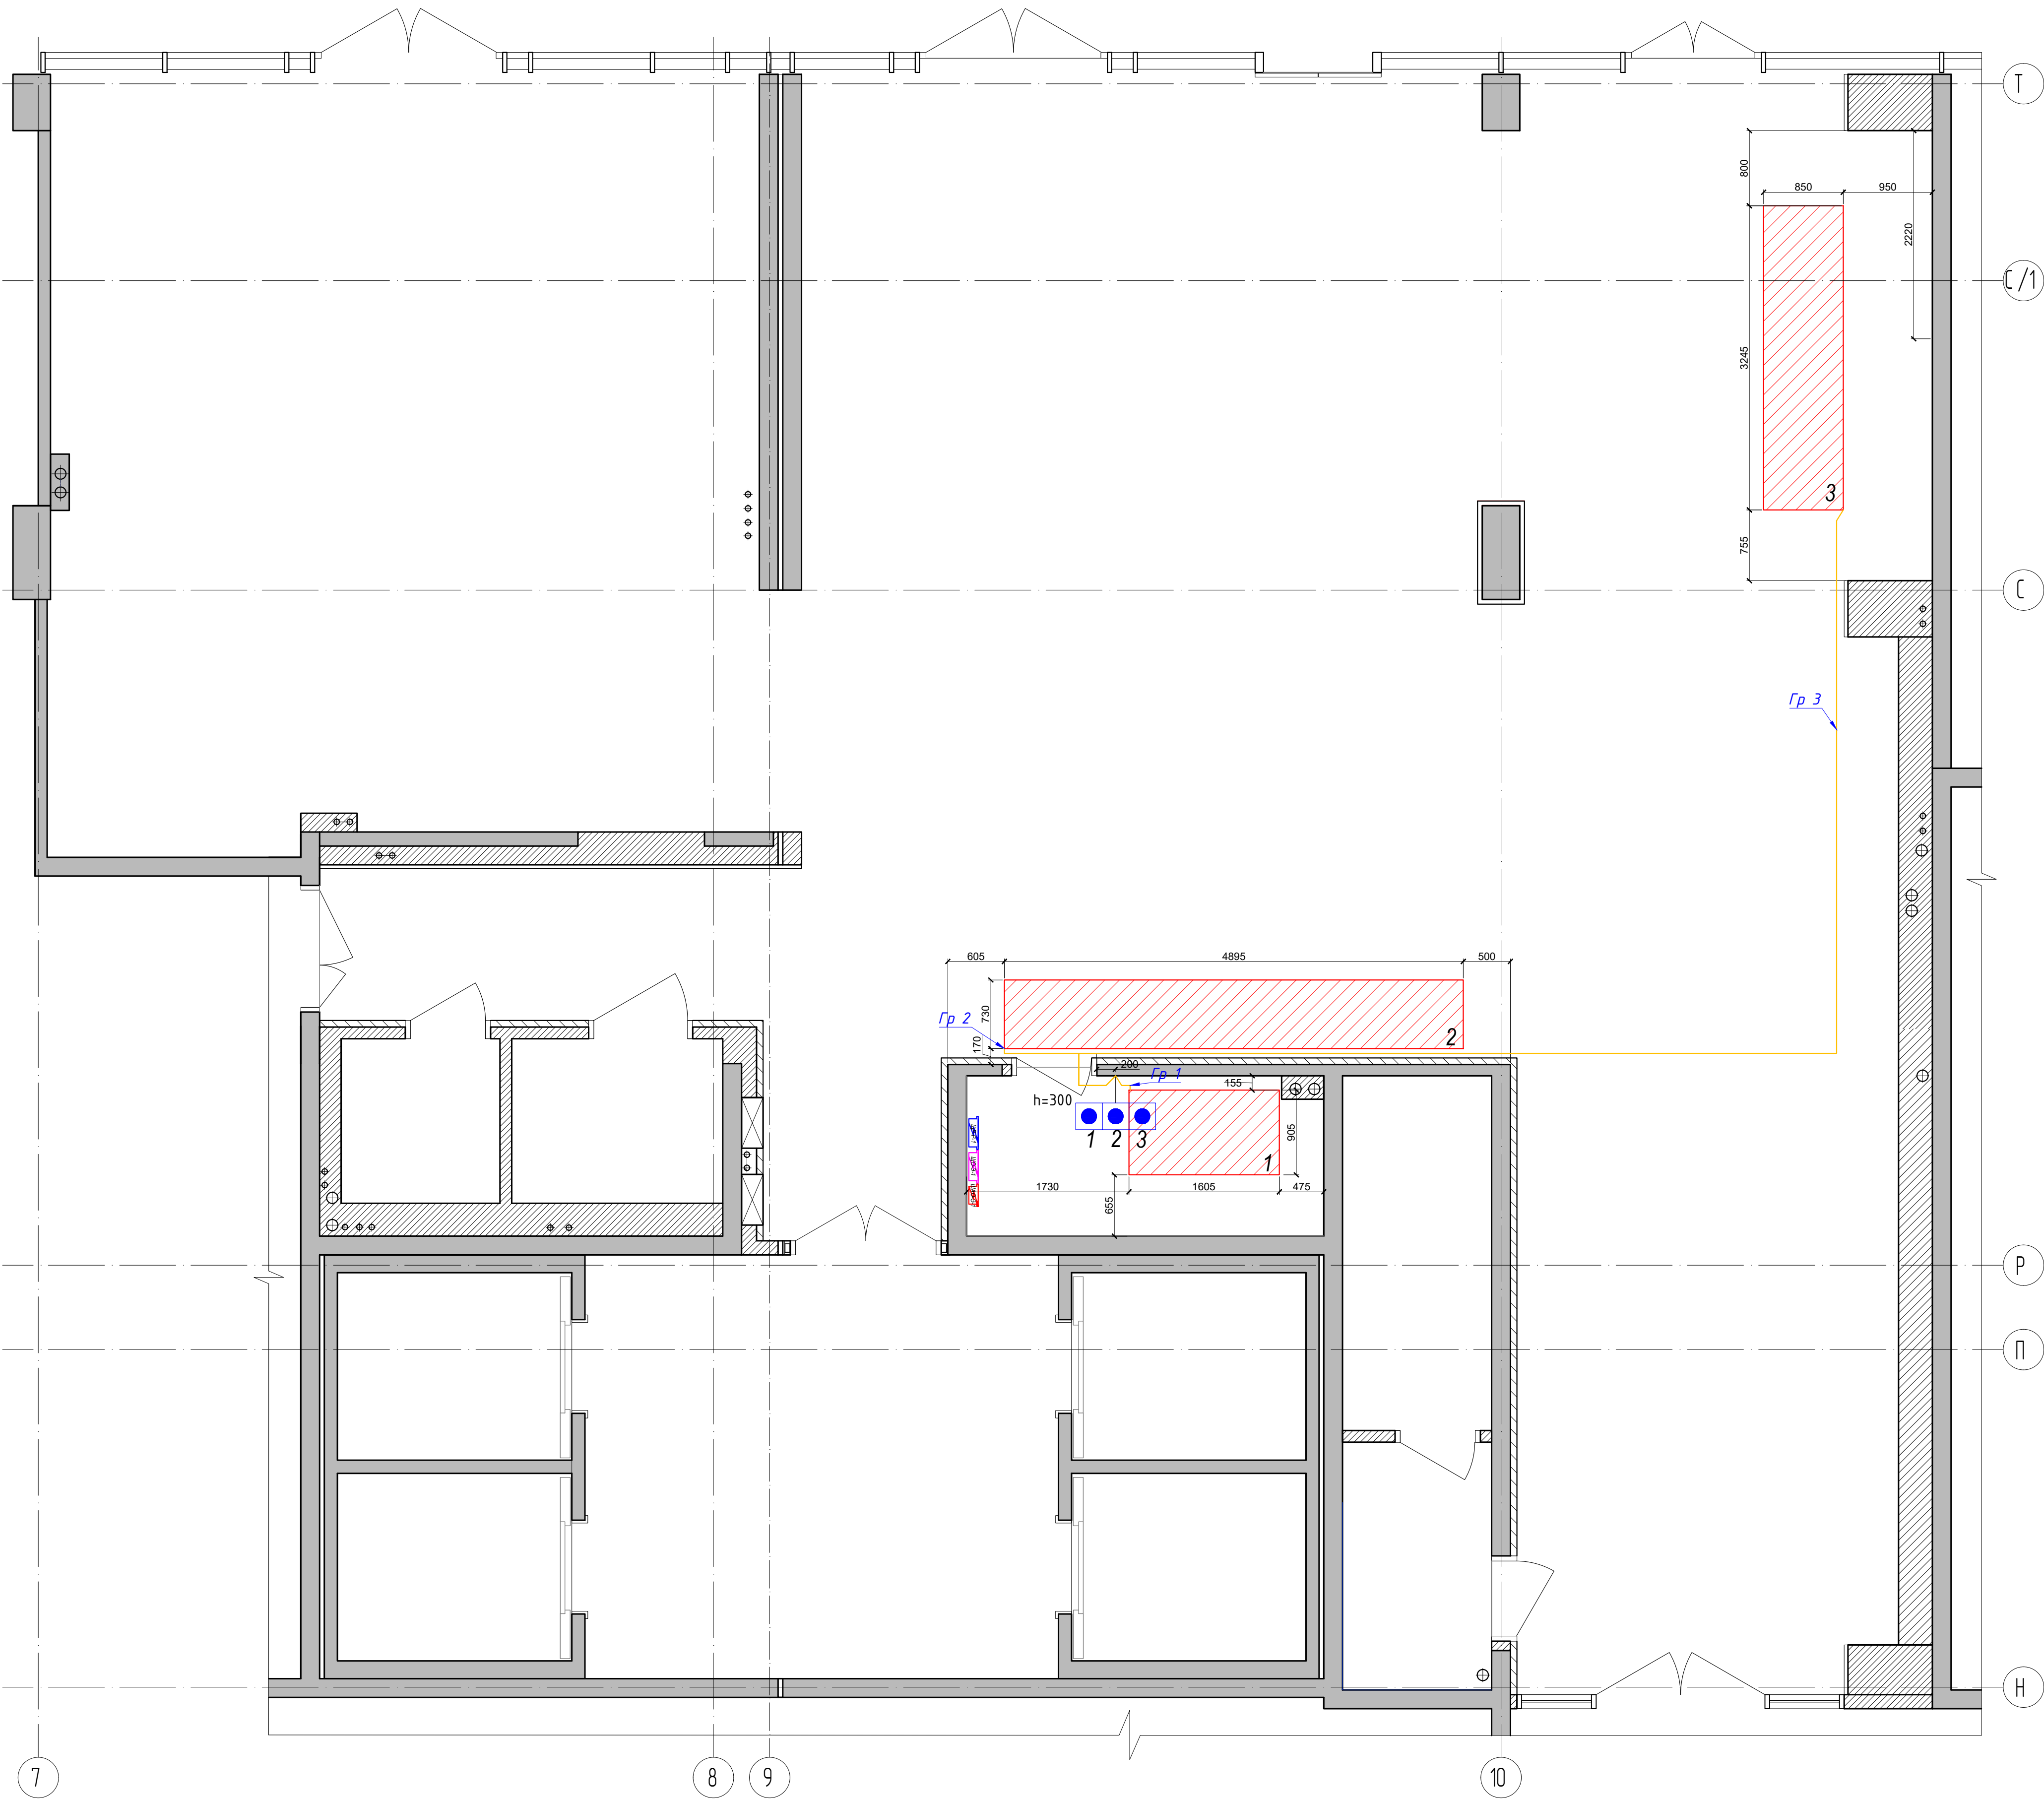


УСЛОВНЫЕ ОБОЗНАЧЕНИЯ


обознач.	Наименование	Кол-во
②	Номер помещения	
	Область пола с электрическим подогревом	7,8 м2
	Регулятор теплого пола, с термодатчиком под плиткой в зоне теплого пола.	3шт.

- ПРИМЕЧАНИЯ:
- 1. Площади материалов даны чистые (без учета запаса).
 - 2. Уточнить размеры после завершения штукатурных работ.
 - 3. Регуляторы теплого пола, с термодатчиком в зоне теплого пола (выносная термопара под плиткой).


						05/2019г.	№ 04.1/АИ-0217					
						Объект: апартаменты. Адрес: г. Санкт-Петербург, ул. Херсонская 8.43/12, лит. А						
Изм.	Кол-во	Лист	№ док.	Подпись	Дата	Интерьерные решения Холл-ресепшн	Стация	Лист	Листов			
Ведущий арх-р			Быков М.М.				Р	9				
Диз-р			Терехин С.В.									
Диз-р												
						План полов с обогревом.	maxdesign					
И контроль			Быков М.М.									

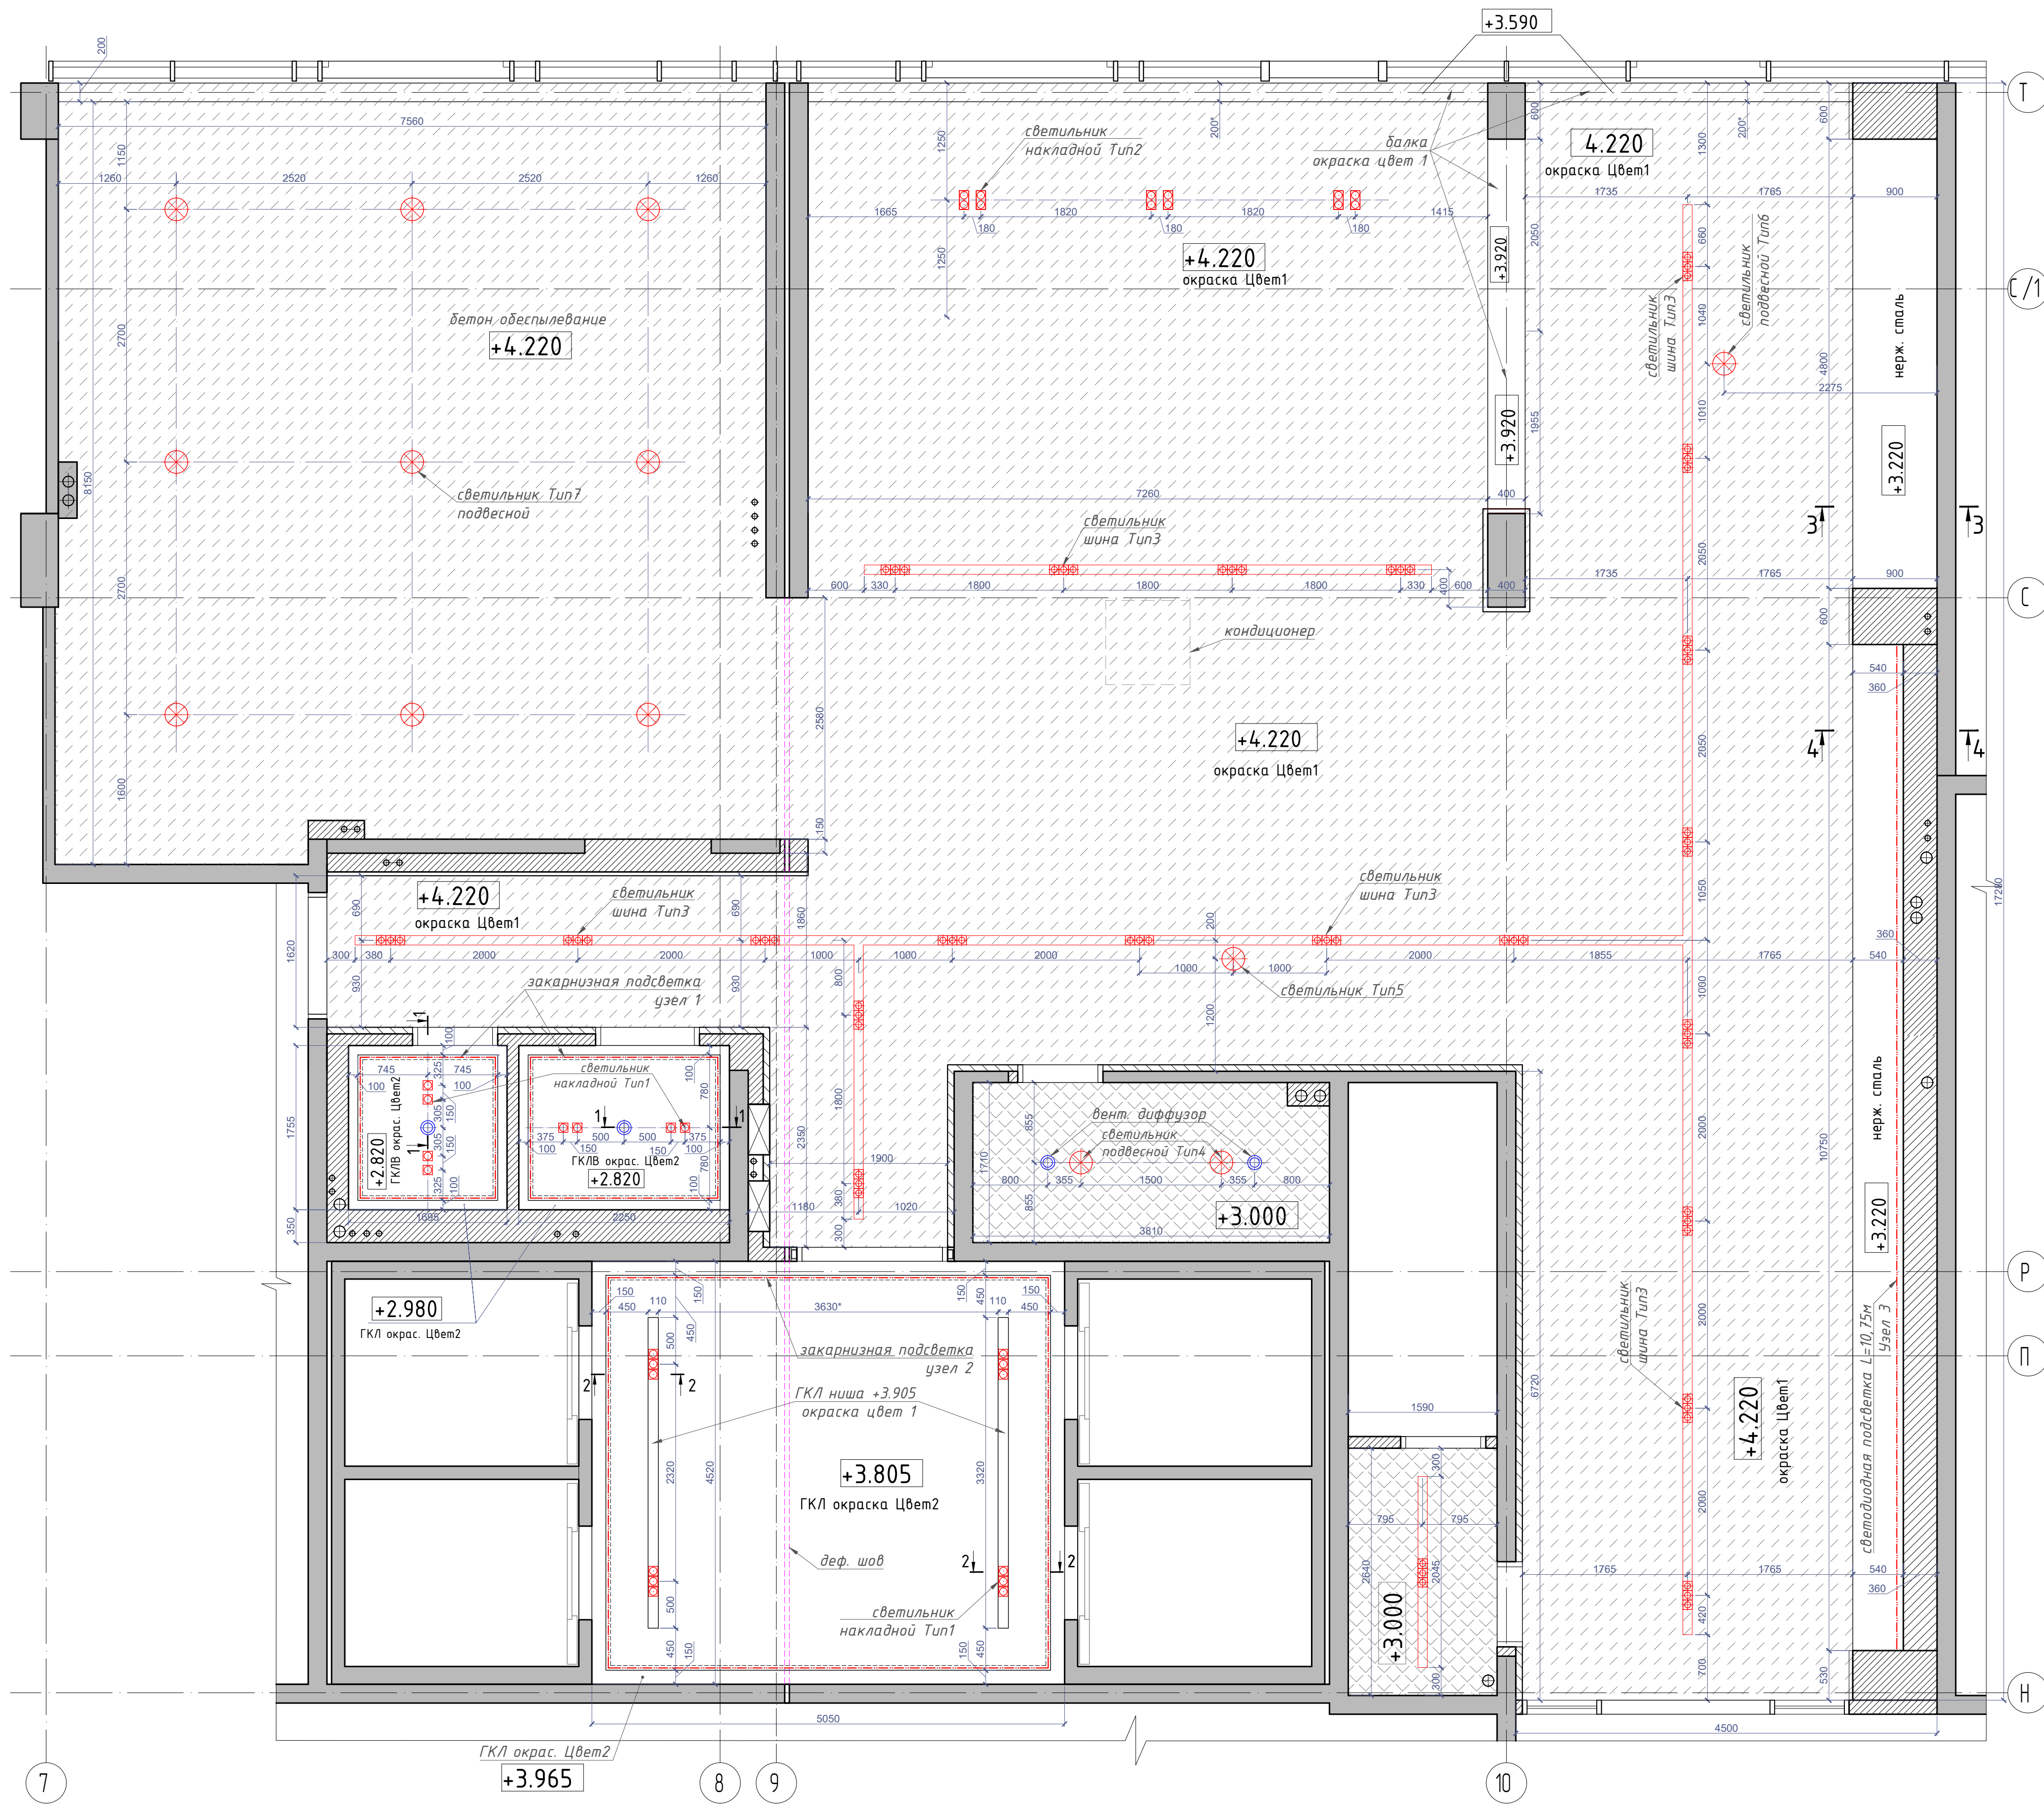


Сечение 1-1 (М1:20)

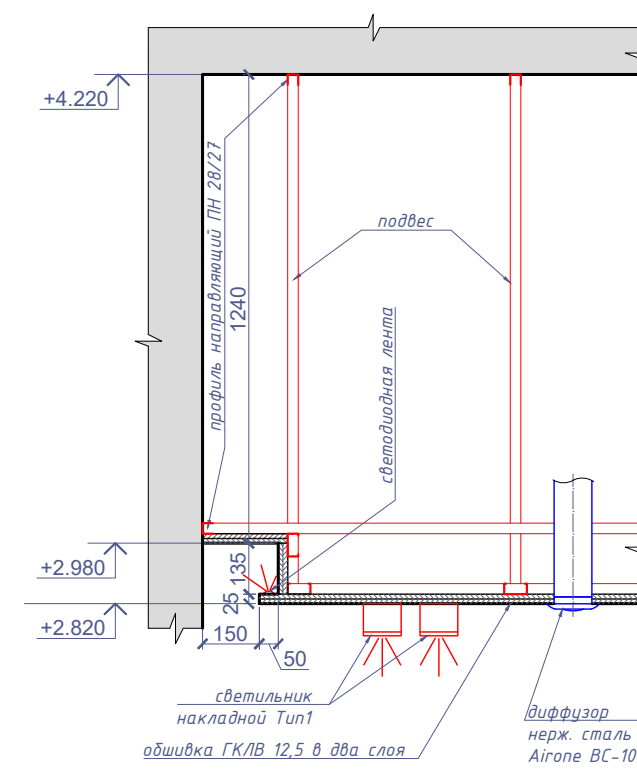


Сечение 2-2 (М1:20)

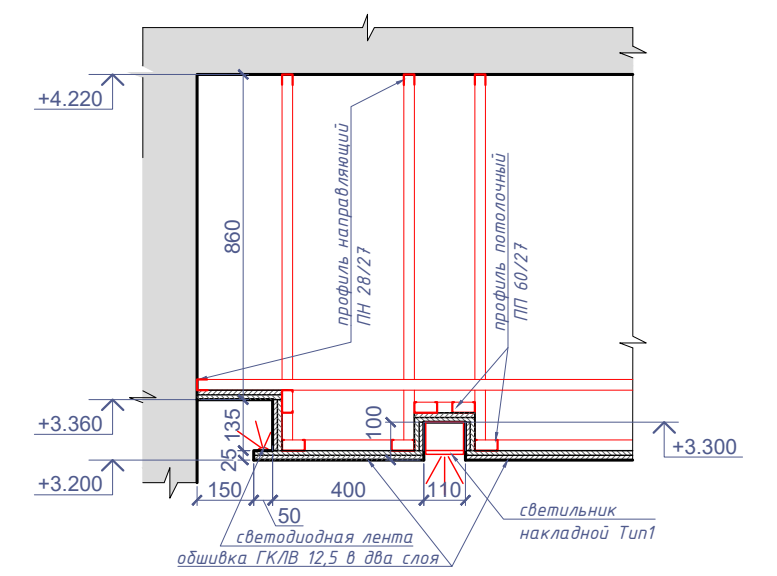

Сечение 3-3 (М1:20)

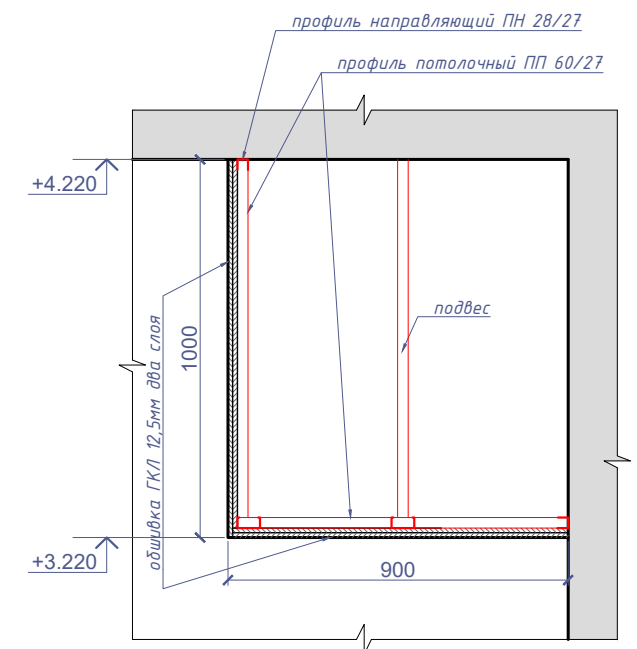

Сечение 4-4 (М1:20)

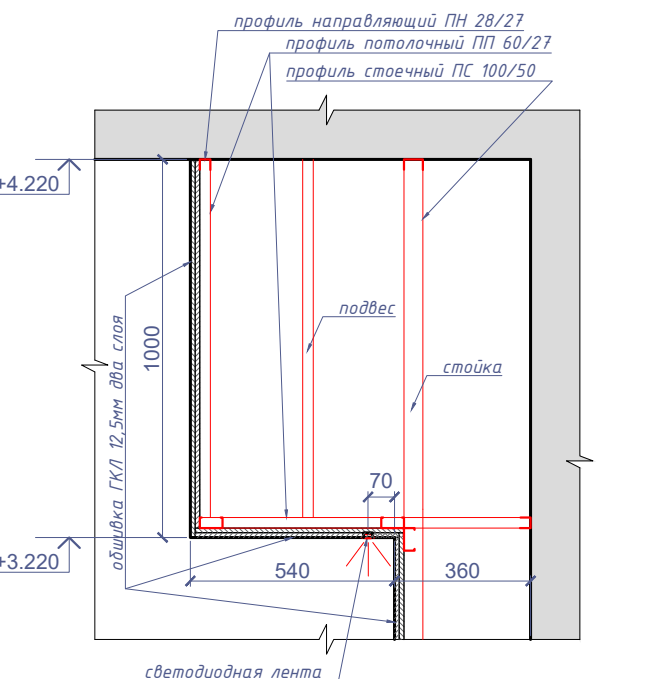

УСЛОВНЫЕ ОБОЗНАЧЕНИЯ

Услов. обознач.	Наименование	Кол-во
	отметка чистого потолка (за 0.000 принята отм. чистого пола)	
	деформационный шов	11,5 м.п.
	светильник Тип 1	20 шт.
	светильник Тип 2	6 шт.
	светильник Тип 3	22 шт.
	светильник Тип 4	2 шт.
	светильник Тип 5	1 шт.
	светильник Тип 6	1 шт.
	светильник Тип 7	9 шт.
	вентиляционный диффузор	4 шт.
	светодиодная лента	41,5 м.п.
	Номер помещения	
	Г/ш. монолит. плита, ошпесыливание, окраска	214 м2
	Г/КЛ потолок, окраска	32 м2
	Потолок подвесной, звукоизоляционный, модульный. Типа Армстронг плита Ultima+ Vector 600x600x19	11 м2

ПРИМЕЧАНИЯ:

1. За отметку 0,000 принята отметка чистого пола первого этажа.
2. Каркас потолка представлен условно. Конкретные решения требуется выбрать из каталога решений фирмы Кнауф.
4. Уточнить размеры после завершения штукатурных работ.
5. Монтаж сети осуществлять ортогональным способом.

						05/2019г.	№ 041/ АИ-0217				
						Объект: апартаменты. Адрес: г. Санкт-Петербург, ул. Херсанская д.43/12, лит. А					
Изм.	Кол-во	Лист	№ док	Подпись	Дата						
Ведущий арх-р	Быков М.М.					Интерьерные решения Холл-ресепши	Стадия	Лист	Листов		
Диз-р	Терехин С.В.						Р	10			
Диз-р											
						План потолка.					
Н контроль.	Быков М.М.										

Technical drawing of a lighting layout for a room, showing various light fixtures, dimensions, and labels in Russian.

Key components and labels:


- светильник накладной Тип2** (Surface-mounted light fixture Type 2)
- светильник Тип7 подвесной** (Hanging light fixture Type 7)
- светильник шина Тип3** (Track light fixture Type 3)
- светодиодная подсветка L=13м.п.** (LED backlighting L=13m)
- светильник накладной Тип1** (Surface-mounted light fixture Type 1)
- светильник Тип5 подвесной** (Hanging light fixture Type 5)
- светильник подвесной Тип4** (Hanging light fixture Type 4)
- светильник накладный Тип3 L=2300** (Surface-mounted light fixture Type 3 L=2300)
- светодиодная подсветка L=17,75м.п.** (LED backlighting L=17.75m)
- светильник накладной Тип1 по 3шт. в группе** (Surface-mounted light fixture Type 1, 3 units per group)
- светодиодная подсветка L=10,75м** (LED backlighting L=10.75m)
- светильник шина Тип3** (Track light fixture Type 3)

The drawing includes detailed dimensions for fixture placement and track lengths, as well as a grid system (A-H, 1-10) for reference.

Услов. обознач.	Наименование	Кол-во
(2)	Номер помещения	
☒	светильник Тип 1 DILSYS DISKO-1	20 шт.
☒	светильник Тип 2 DILSYS DISKO-1 группа из 2х штук	6 шт.
☒	светильник Тип 3 DILSYS ROLL-S 10 группа из 3х штук	21 шт.
☒	светильник Тип 4 Arte lamp brassio, черный D= 300-400мм	4 шт.
	светильник Тип 5 CLASSICON Selene Lamp группа из: D~350мм - 12 шт. D~200мм - 25 шт.	1 шт.
	светильник Тип 6 XAL curve L(периметр)= ~7м	1 шт.
	светильник Тип 7 - на усмотрение арендатора	9 шт.
- - -	светодиодная лента Алрайт ARL 10000 PGS - теплый белый свет	4,5 м.п.
▬	светильник настенный Тип8 SIGHT 115 SLV Elektronik 2017 160190 L= 1,2м	2 шт.

1. Расстояния указываются до центра осветительного прибора или центра группы.
2. Все размеры и привязки даны без учета отступов от стен для отделки (по 10 мм. на отделку плиткой).
3. Данный лист смотреть совместно с листом "План потолка".

						05/2019г.	№04/1/ АИ-0217		
							Объект: апартаменты. Адрес: г. Санкт-Петербург, ул. Херсонская д.43/12, лит. А		
Изм.	Колуч	Лист	№ док	Подпись	Дата				
Ведущий арх-р	Быков М.М.						Стадия	Лист	Листов
Диз-р	Терехин С.В.					Интерьерные решения Холл-ресепши	Р	11	
Диз-р									
						План расположения осветительных приборов.	maxdesign		
Н.констр.	Быков М.М.								

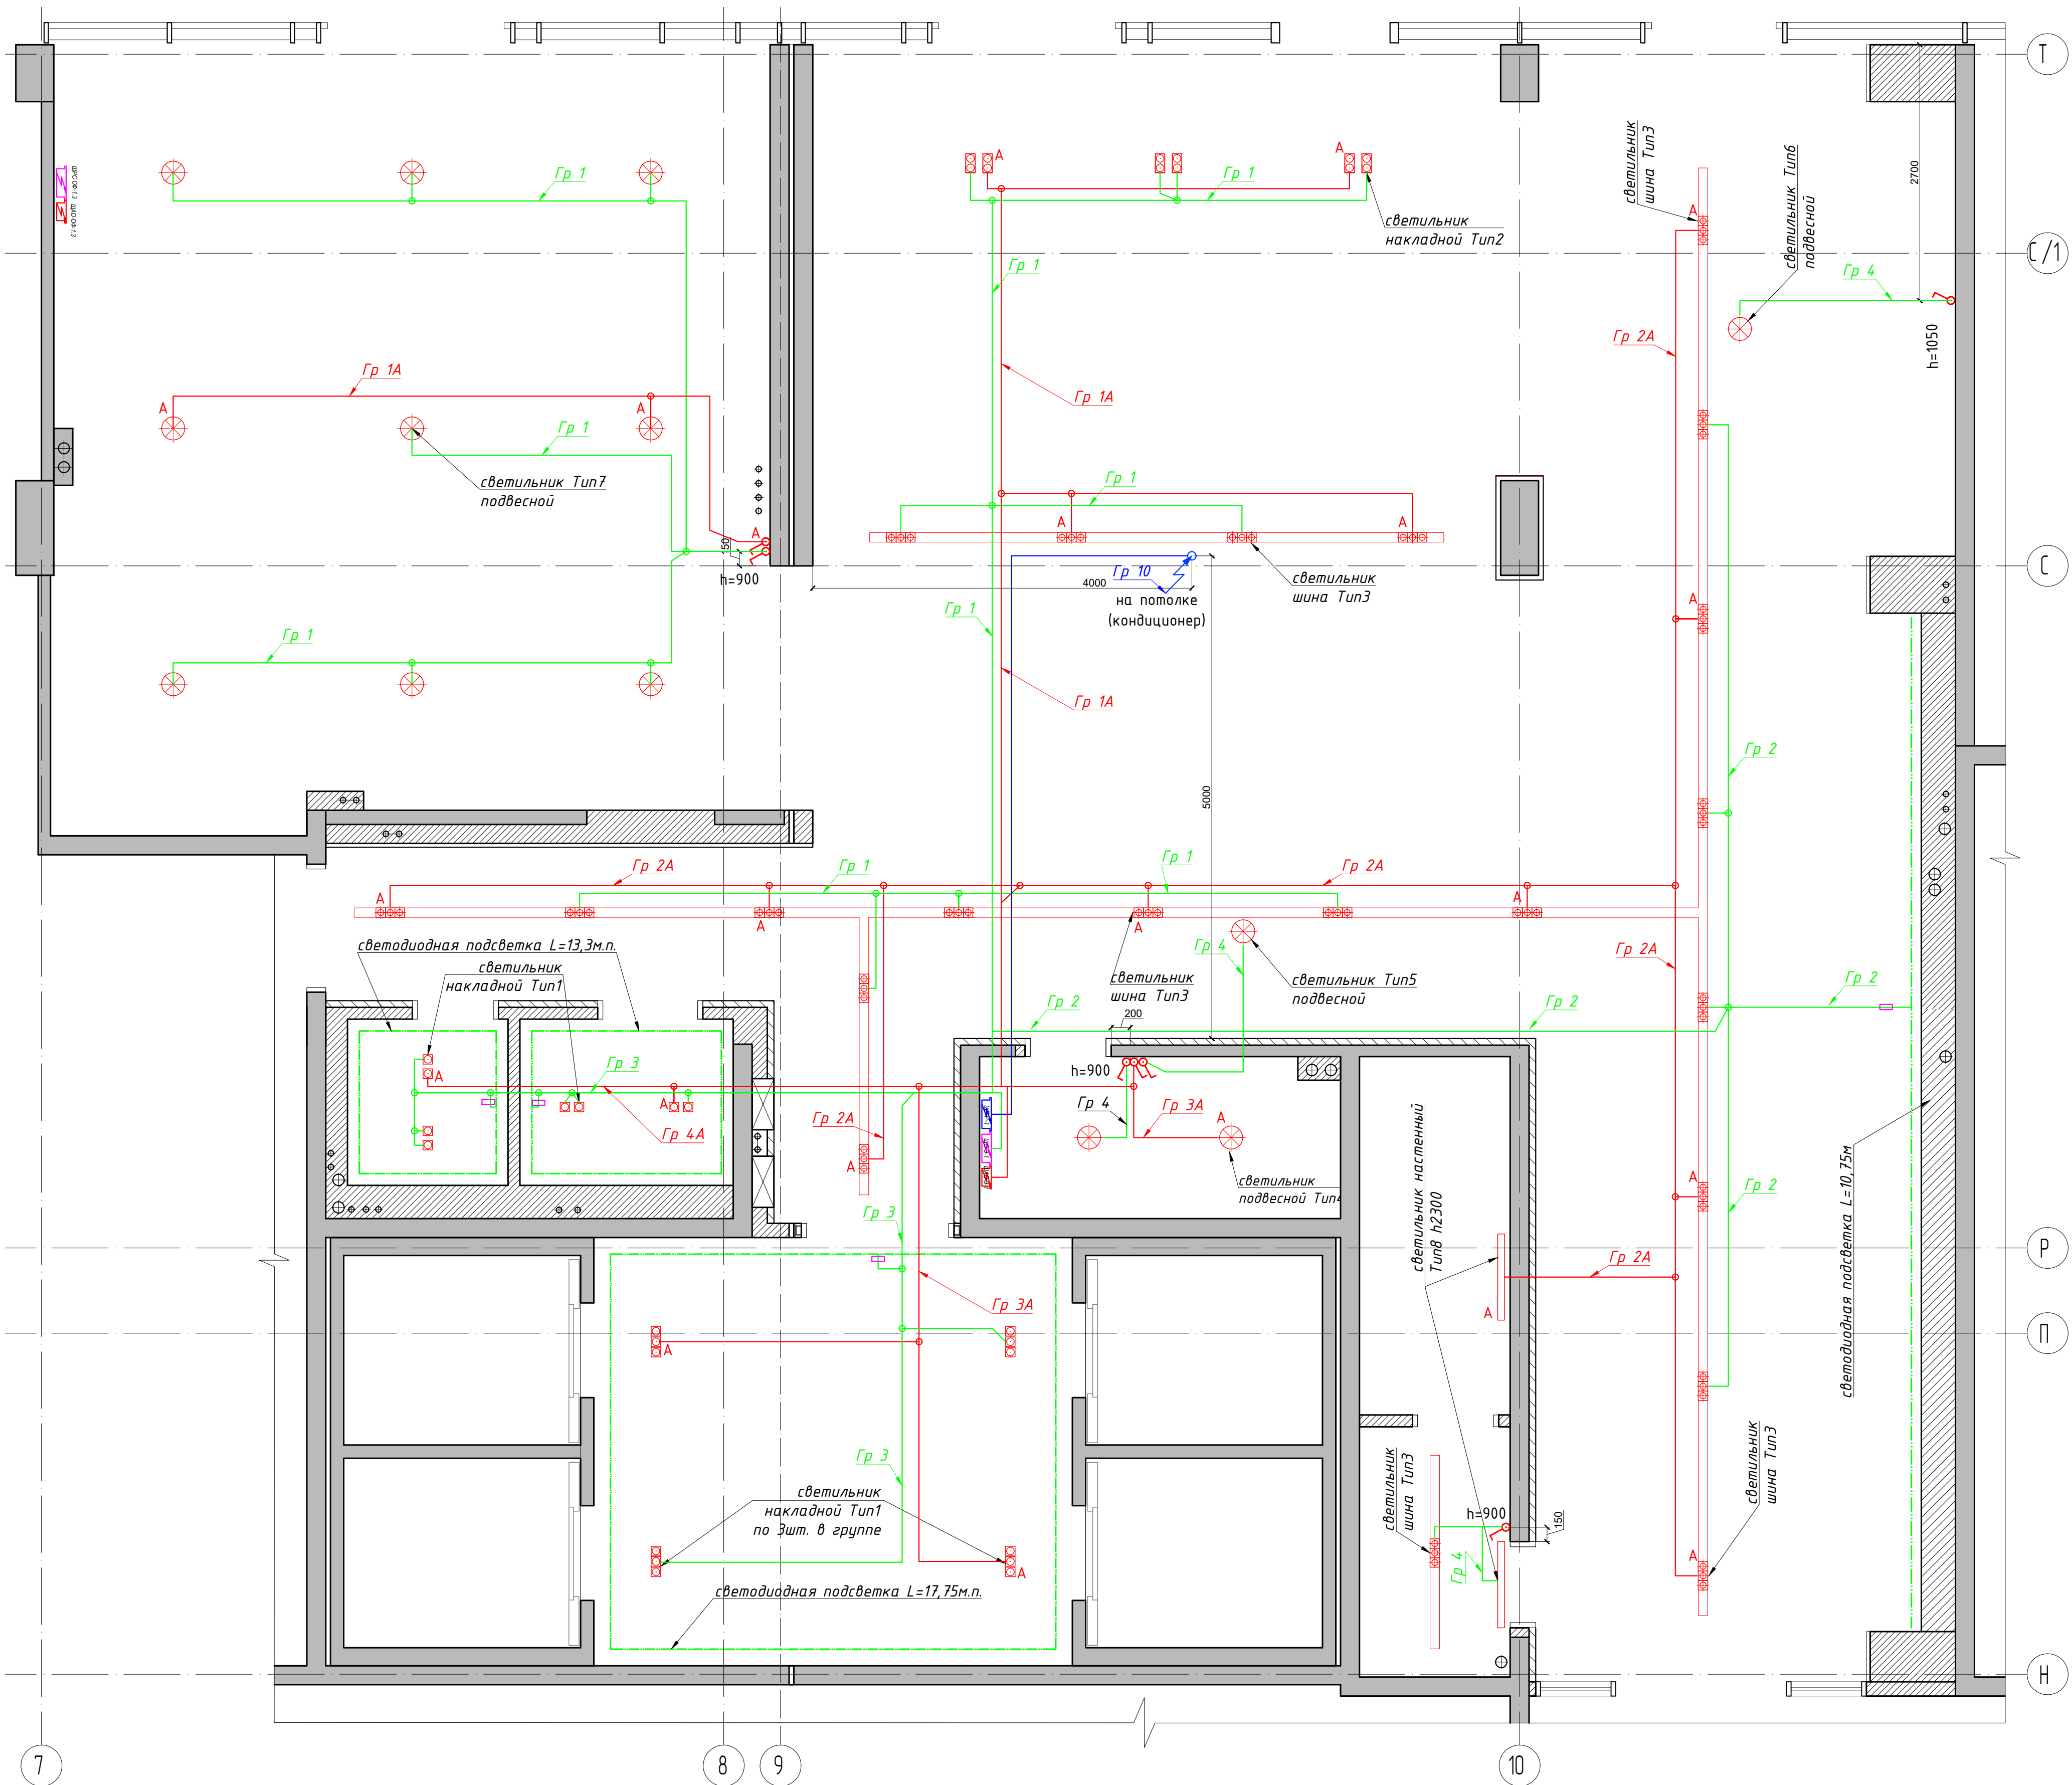


УСЛОВНЫЕ ОБОЗНАЧЕНИЯ

Услов. обознач.	Наименование	Кол-во
□	светильник Тип 1	20 шт.
□	светильник Тип 2	6 шт.
□	светильник Тип 3	21 шт.
⊗	светильник Тип 4	2 шт.
	светильник Тип 5	1 шт.
	светильник Тип 6	1 шт.
	светильник Тип 7	9 шт.
—	светильник настенный Тип 8	2 шт.
—	светодиодная лента	41,5 м.п.
—	группы аварийного освещения	
—	группы основного освещения	
⌋	выключатель одноклавишный	7 шт.

ПРИМЕЧАНИЯ:

1. Данная схема содержит информацию о логических группах включения и не отображает реального, фактического способа прокладки кабеля.
3. Расстояния указываются до центра электрического прибора или центра группы.
4. Все размеры и привязки даны без учета отступов от стен для отделки.
5. Группа основного и аварийного освещения управляется с главного пульта диспетчера.

					05/2019г.	№ 04.1/АИ-0217
					Объект: апартаменты. Адрес: г. Санкт-Петербург, ул. Херсонская д.43/12, лит. А	
Изм.	Копия	Лист	№ док.	Подпись	Дата	
Ведущий арх-р	Быков М.М.					Интерьерные решения Холл-ресепшн
Диз-р	Терехин С.В.					Статия
Диз-р						Лист
						12
						Схема привязки осветительных приборов к выключателям.
Н контроль	Быков М.М.					maxdesign

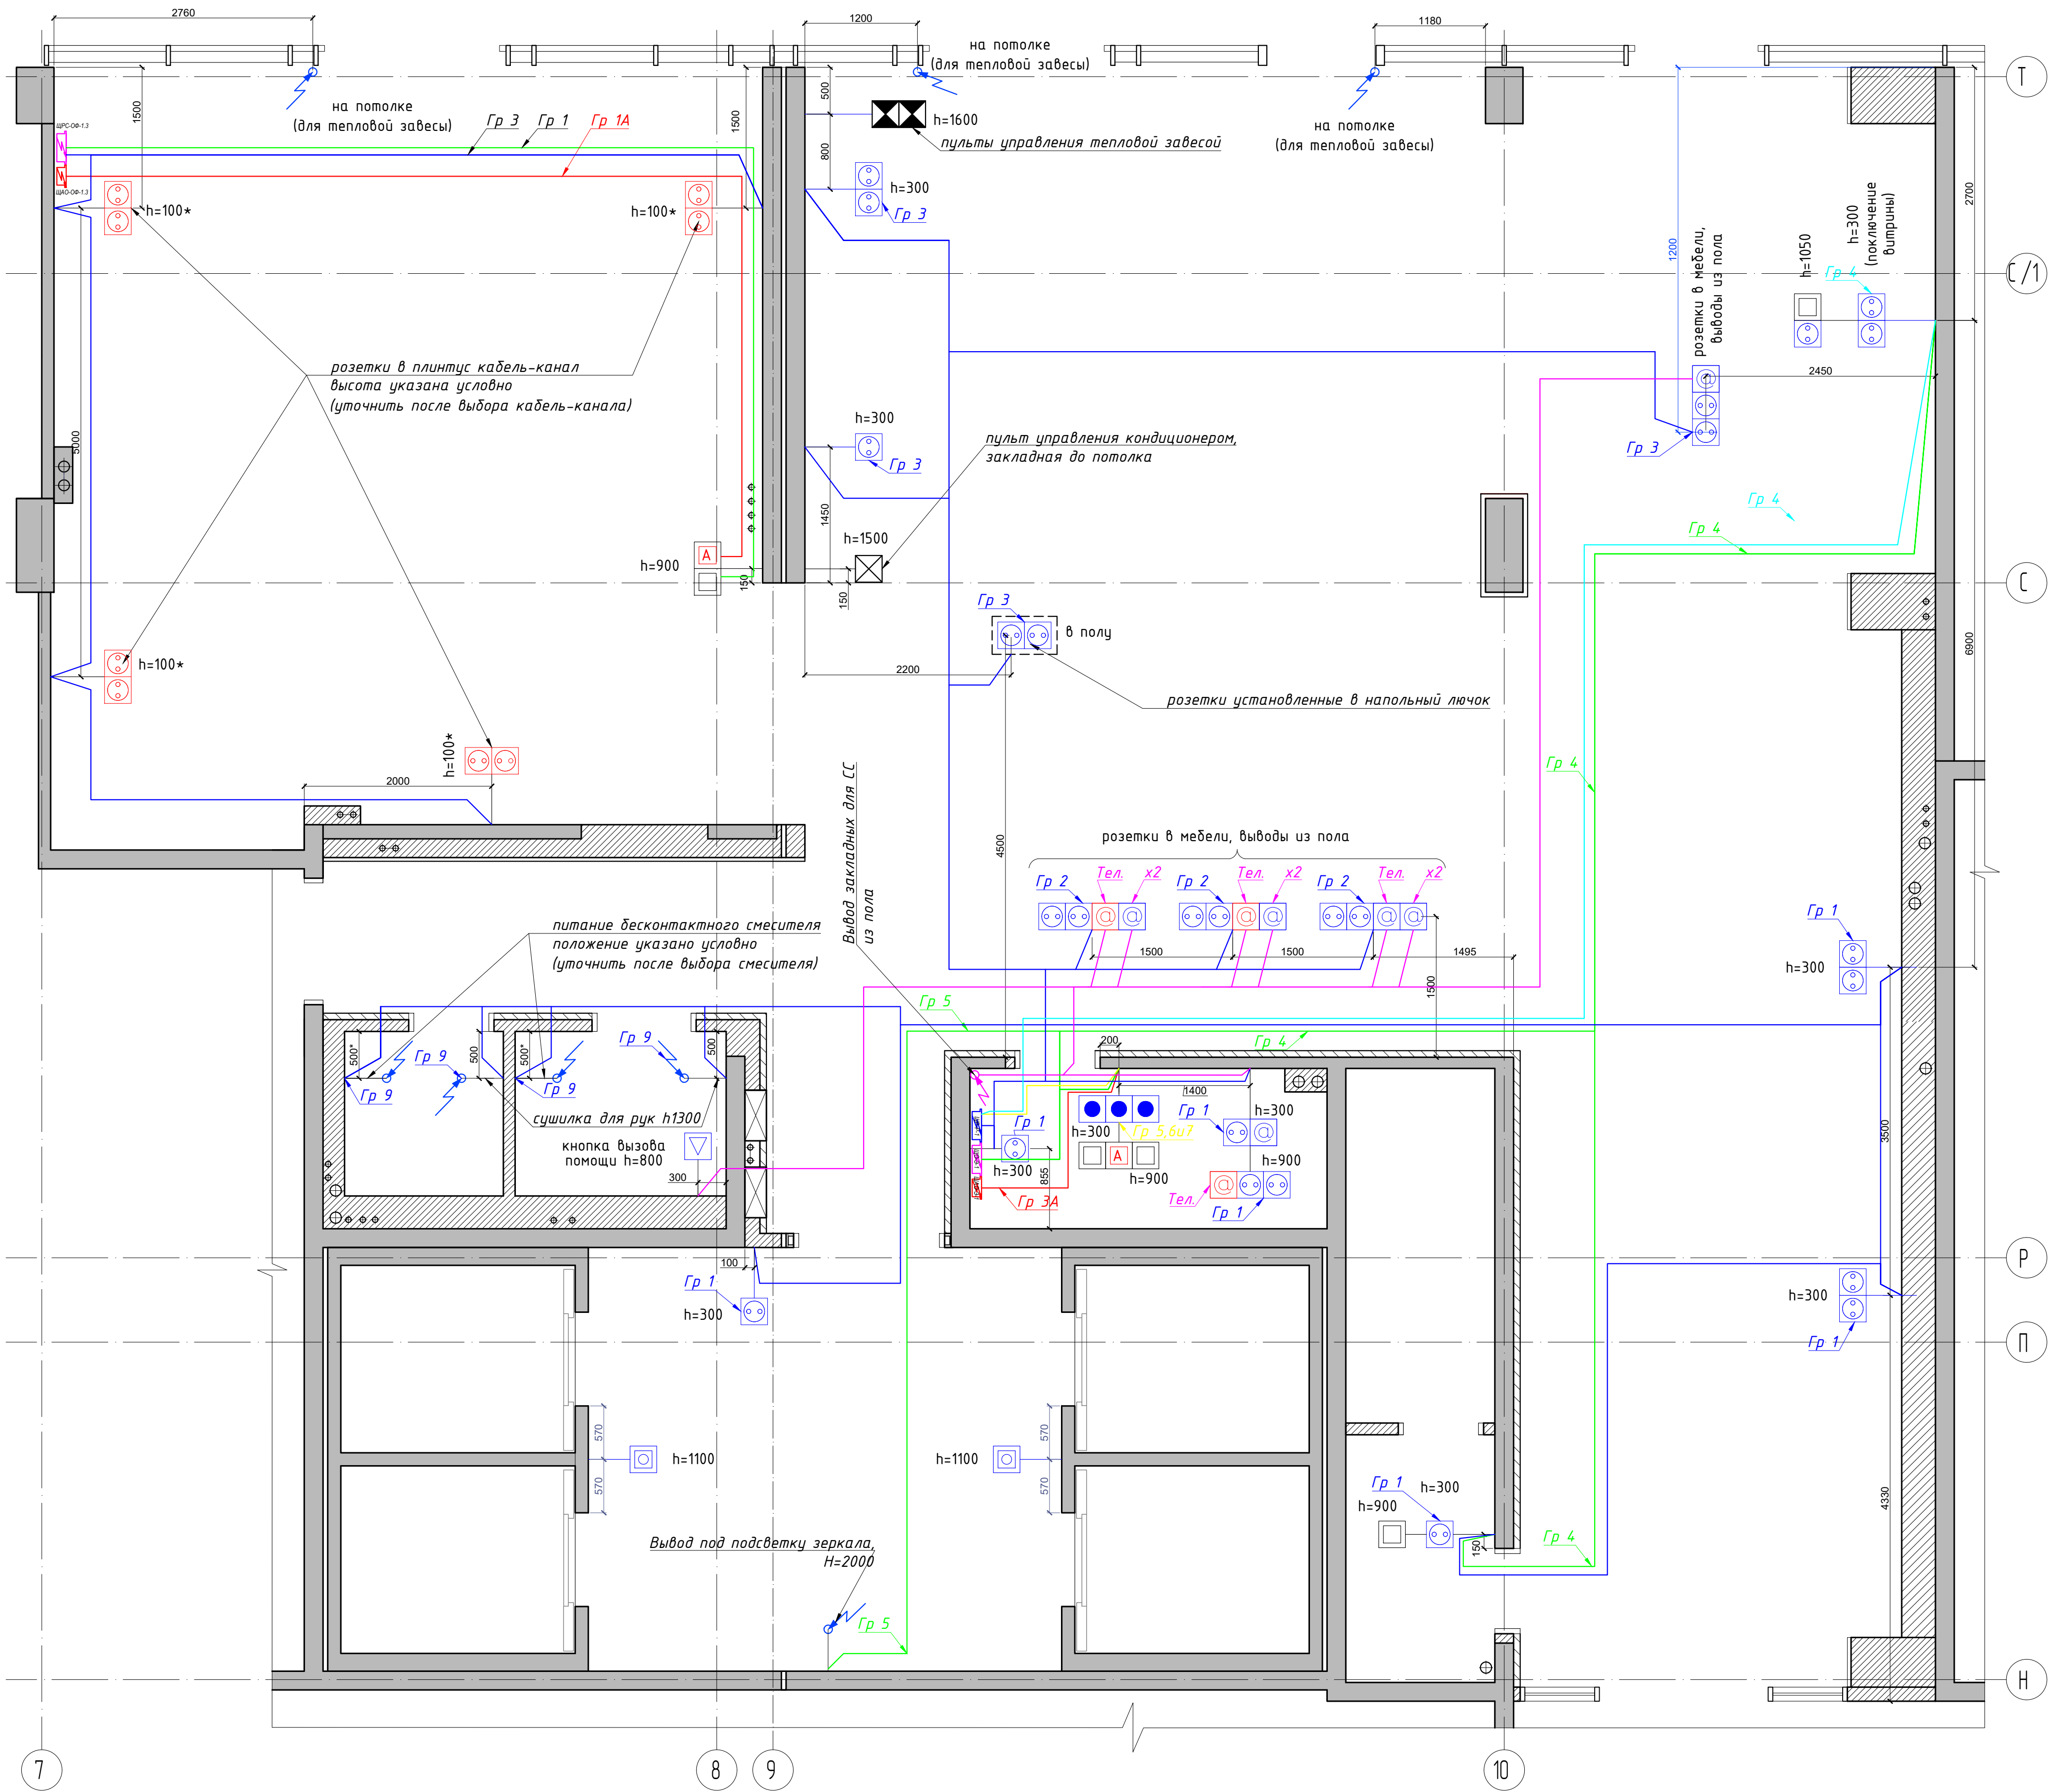


Спецификация оборудования

Услов. обознач.	Наименование	Кол-во
	- розетка 220 вольт	26шт.
	- розетка 220 вольт, встроена в плинтус кабель-канал	8шт.
	- розетка RJ-45	6шт.
	- розетка телефонная RJ-12	3шт.
	- выключатель одноклавишный	5шт.
	- встраиваемый в пол лючок для розеток	1шт.
	- электрический вывод (длина 2м)	
	- кнопка вызова помощи для инвалидов	1шт.
	- кнопка вызова лифта	2шт.
	- пульт управления кондиционером	1шт.
	- регулятор теплого пола с выносным датчиком	3шт.
	- пульт тепловой завесы	2шт.
	- рамка одинарная	5шт.
	- рамка двойная	7шт.
	- рамка тройная	4шт.
	- рамка четверная	3шт.

- ПРИМЕЧАНИЯ:
- Высота всех розеток 300 мм. от уровня пола, если не указано иное на плане.
 - Все отметки даны от чистого пола. Все отметки и размеры указываются до центра рамки розеток.
 - Все размеры и привязки даны без учета отступов от стен для отделки.
 - Высоты каждой розетки и их схему расположения в обязательном порядке сверять с высотами розеток на развертках стен.
 - Данный лист смотреть вместе с листами разверток стен.
 - Сигнал с кнопки вызова помощи для инвалидов вывести на пульт диспетчера.
 - Предусмотреть питание бесконтактных смесителей в санузлах.
 - Проводку на стенах выполнять скрытым способом в (в штробах).
 - Пульты управления тепловыми завесами выполнять врезным способом (в штробе).
 - Вся электроаппаратура производства - Schneider Electric, серия - ATLAS DESIGN цвет - антрацит.

						05/2019г.			№ 04.1/АИ-0217			
						Объект: апартамент-отель. Адрес: г. Санкт-Петербург, ул. Херсонская д.43/12, лит. А						
Изм.	Копия	Лист	№ док.	Подпись	Дата	Интерьерные решения Холл-ресепшин	Стадия	Лист	Листов			
Ведущий арх-р			Быков М.М.				Р	13				
Диз-р			Терехин С.В.									
Диз-р												
						План размещения электрических розеток и электровыводов.	maxdesign					
Н.контр.оль			Быков М.М.									

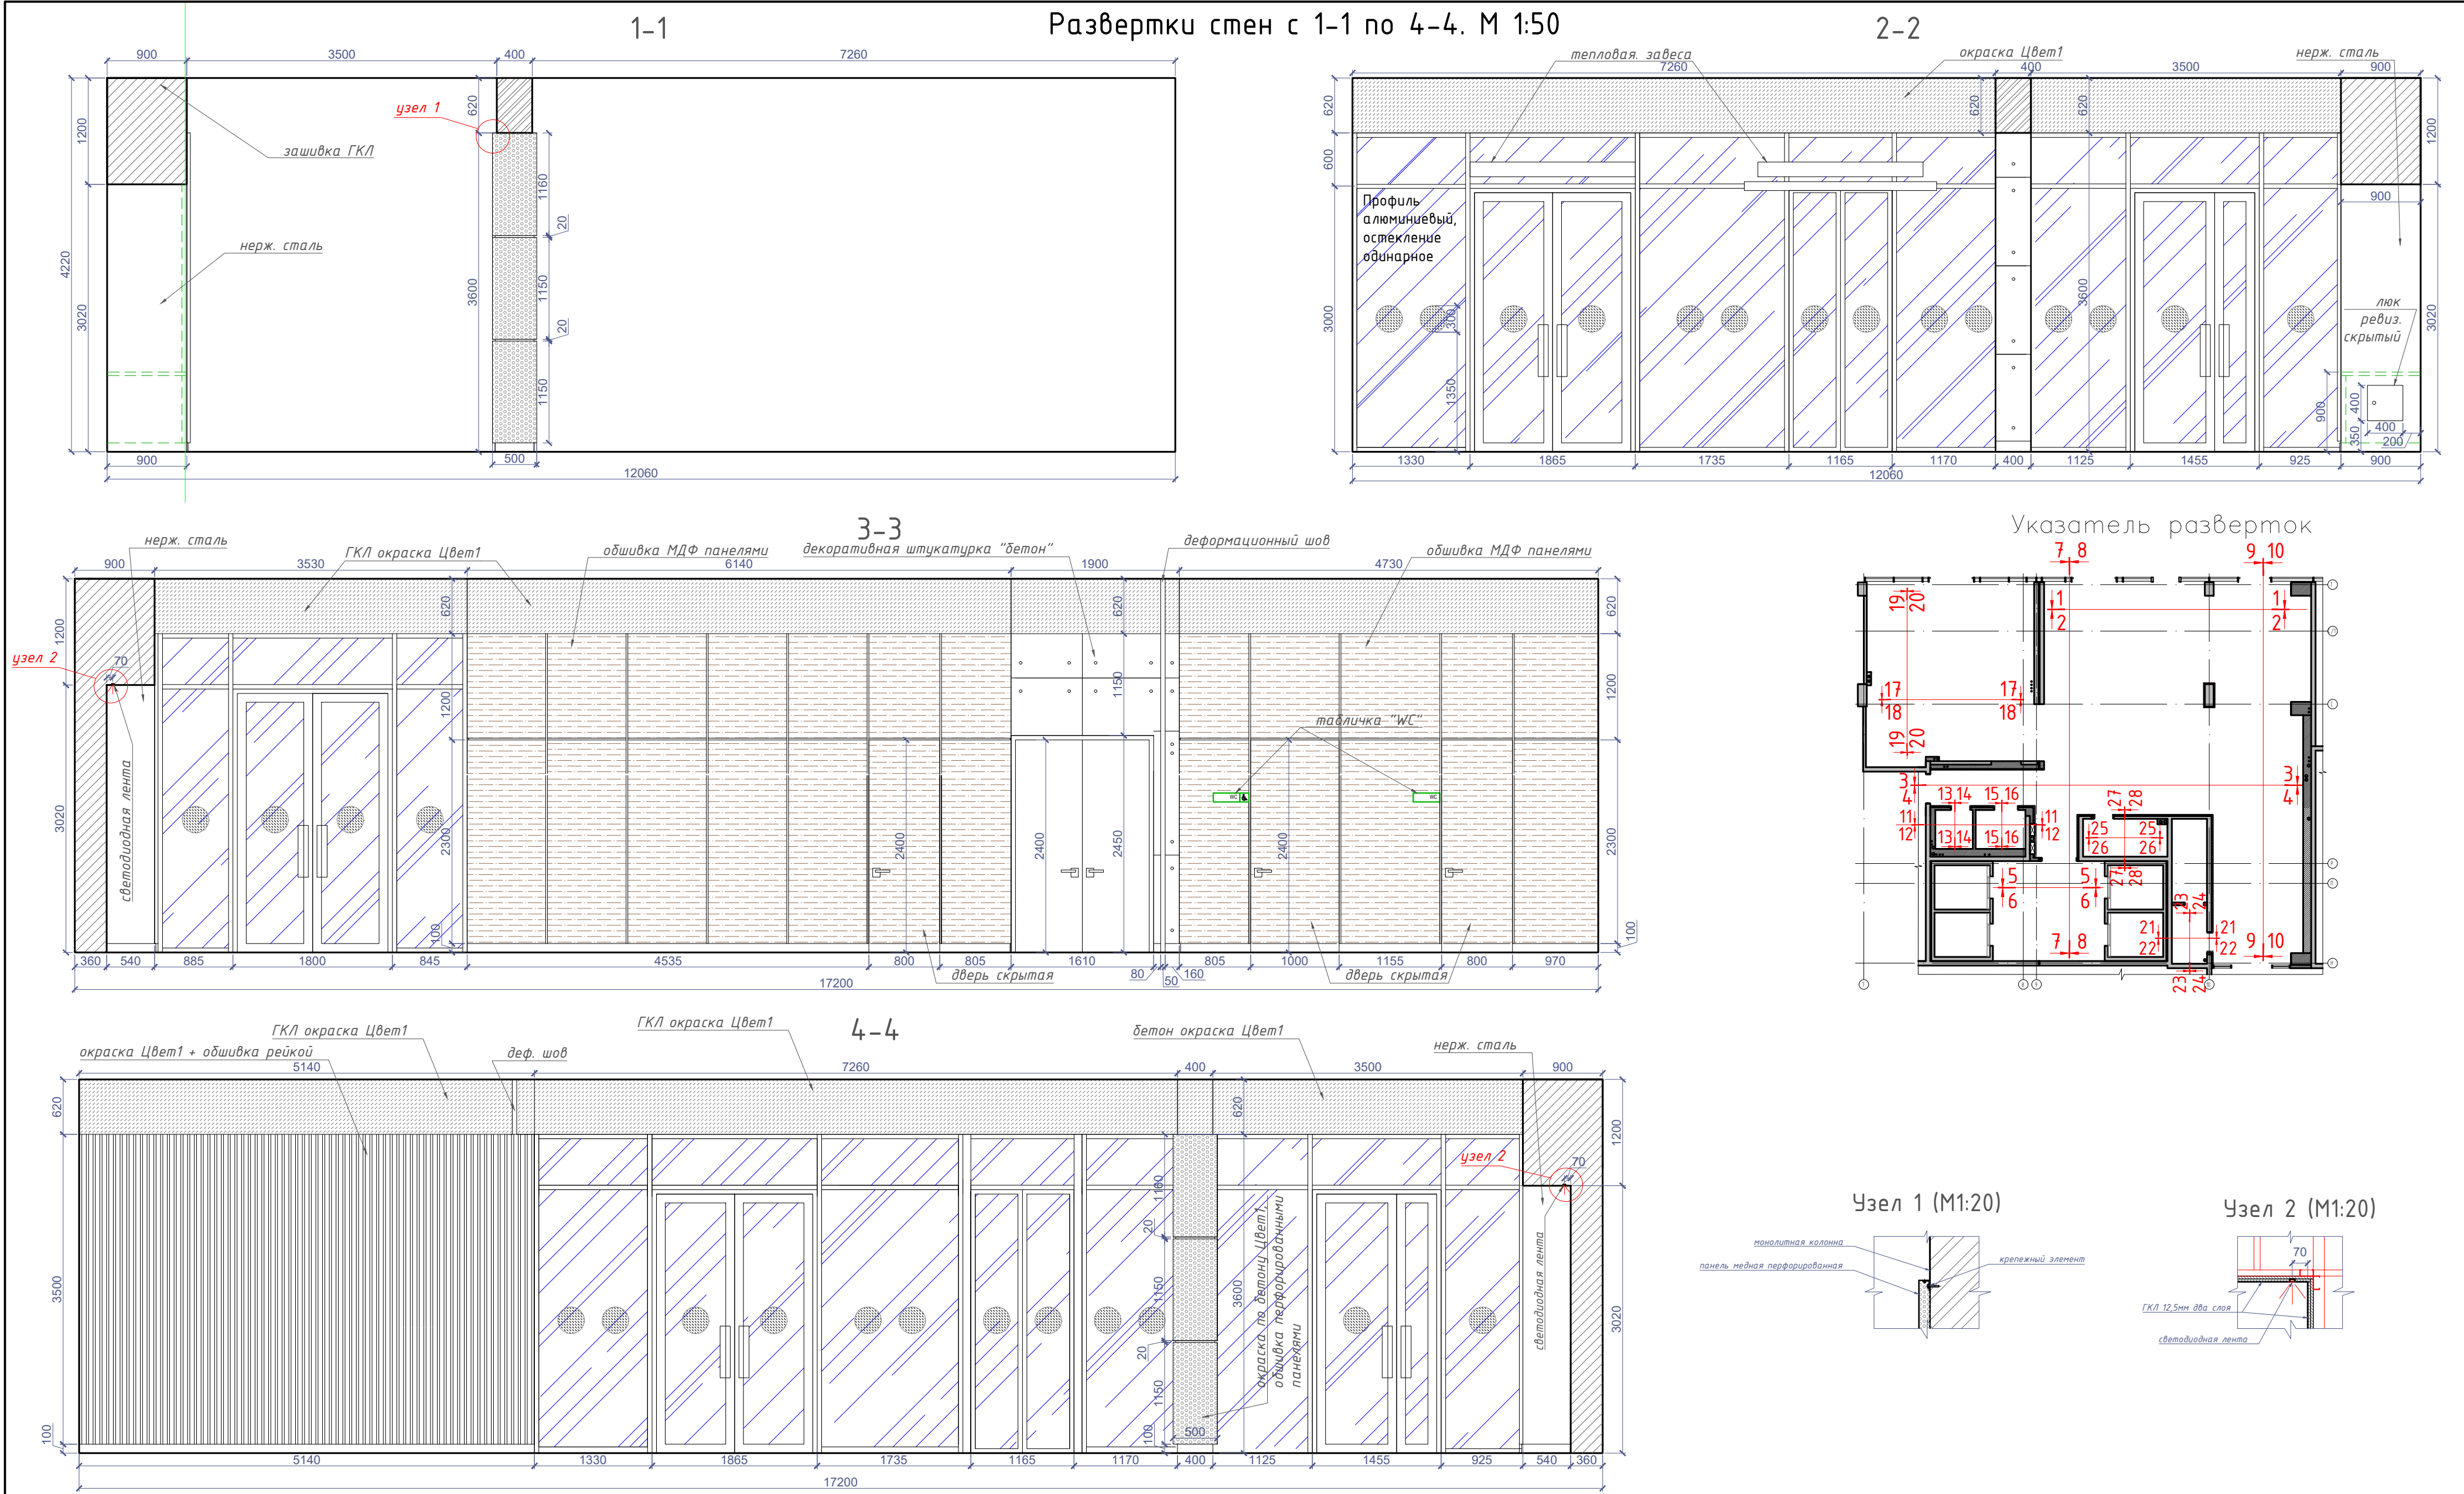


ПРИМЕЧАНИЯ:


- План выполнен по черновым размерам помещений. Требуется корректировка размеров после проведения монтажных работ и чистовой отделки!
- Мебель на заказ устанавливается фирмой-изготовителем только после дополнительно снятых обмеров специалистами.
- Цвета по RAL указаны условно, согласовать выкраски с дизайнерам производящим авторский надзор.
- Размер и положение ревизионных люков уточнить по фактической необходимости.
- Данный лист смотреть совместно с листом 3 "Схема разверток стен".

						05/2019г.				№041/АИ-0217		
						Объект: апартамент-отель. Адрес: г. Санкт-Петербург, ул. Херсонская д.43/12, лит. А						
Изм.	Колуч	Лист	№ док	Подпись	Дата	Интерьерные решения Холл-ресепшн			Стадия	Лист	Листов	
Ведущий арх-р	Быков М.М.								Р	14		
Диз-р	Терехин С.В.											
Диз-р												
						Развертки стен с 1-1 по 4-4. М 1:50			maxdesign			
Н контроль	Быков М.М.											


Развертки стен с 5-5 по 8-8. М 1:50

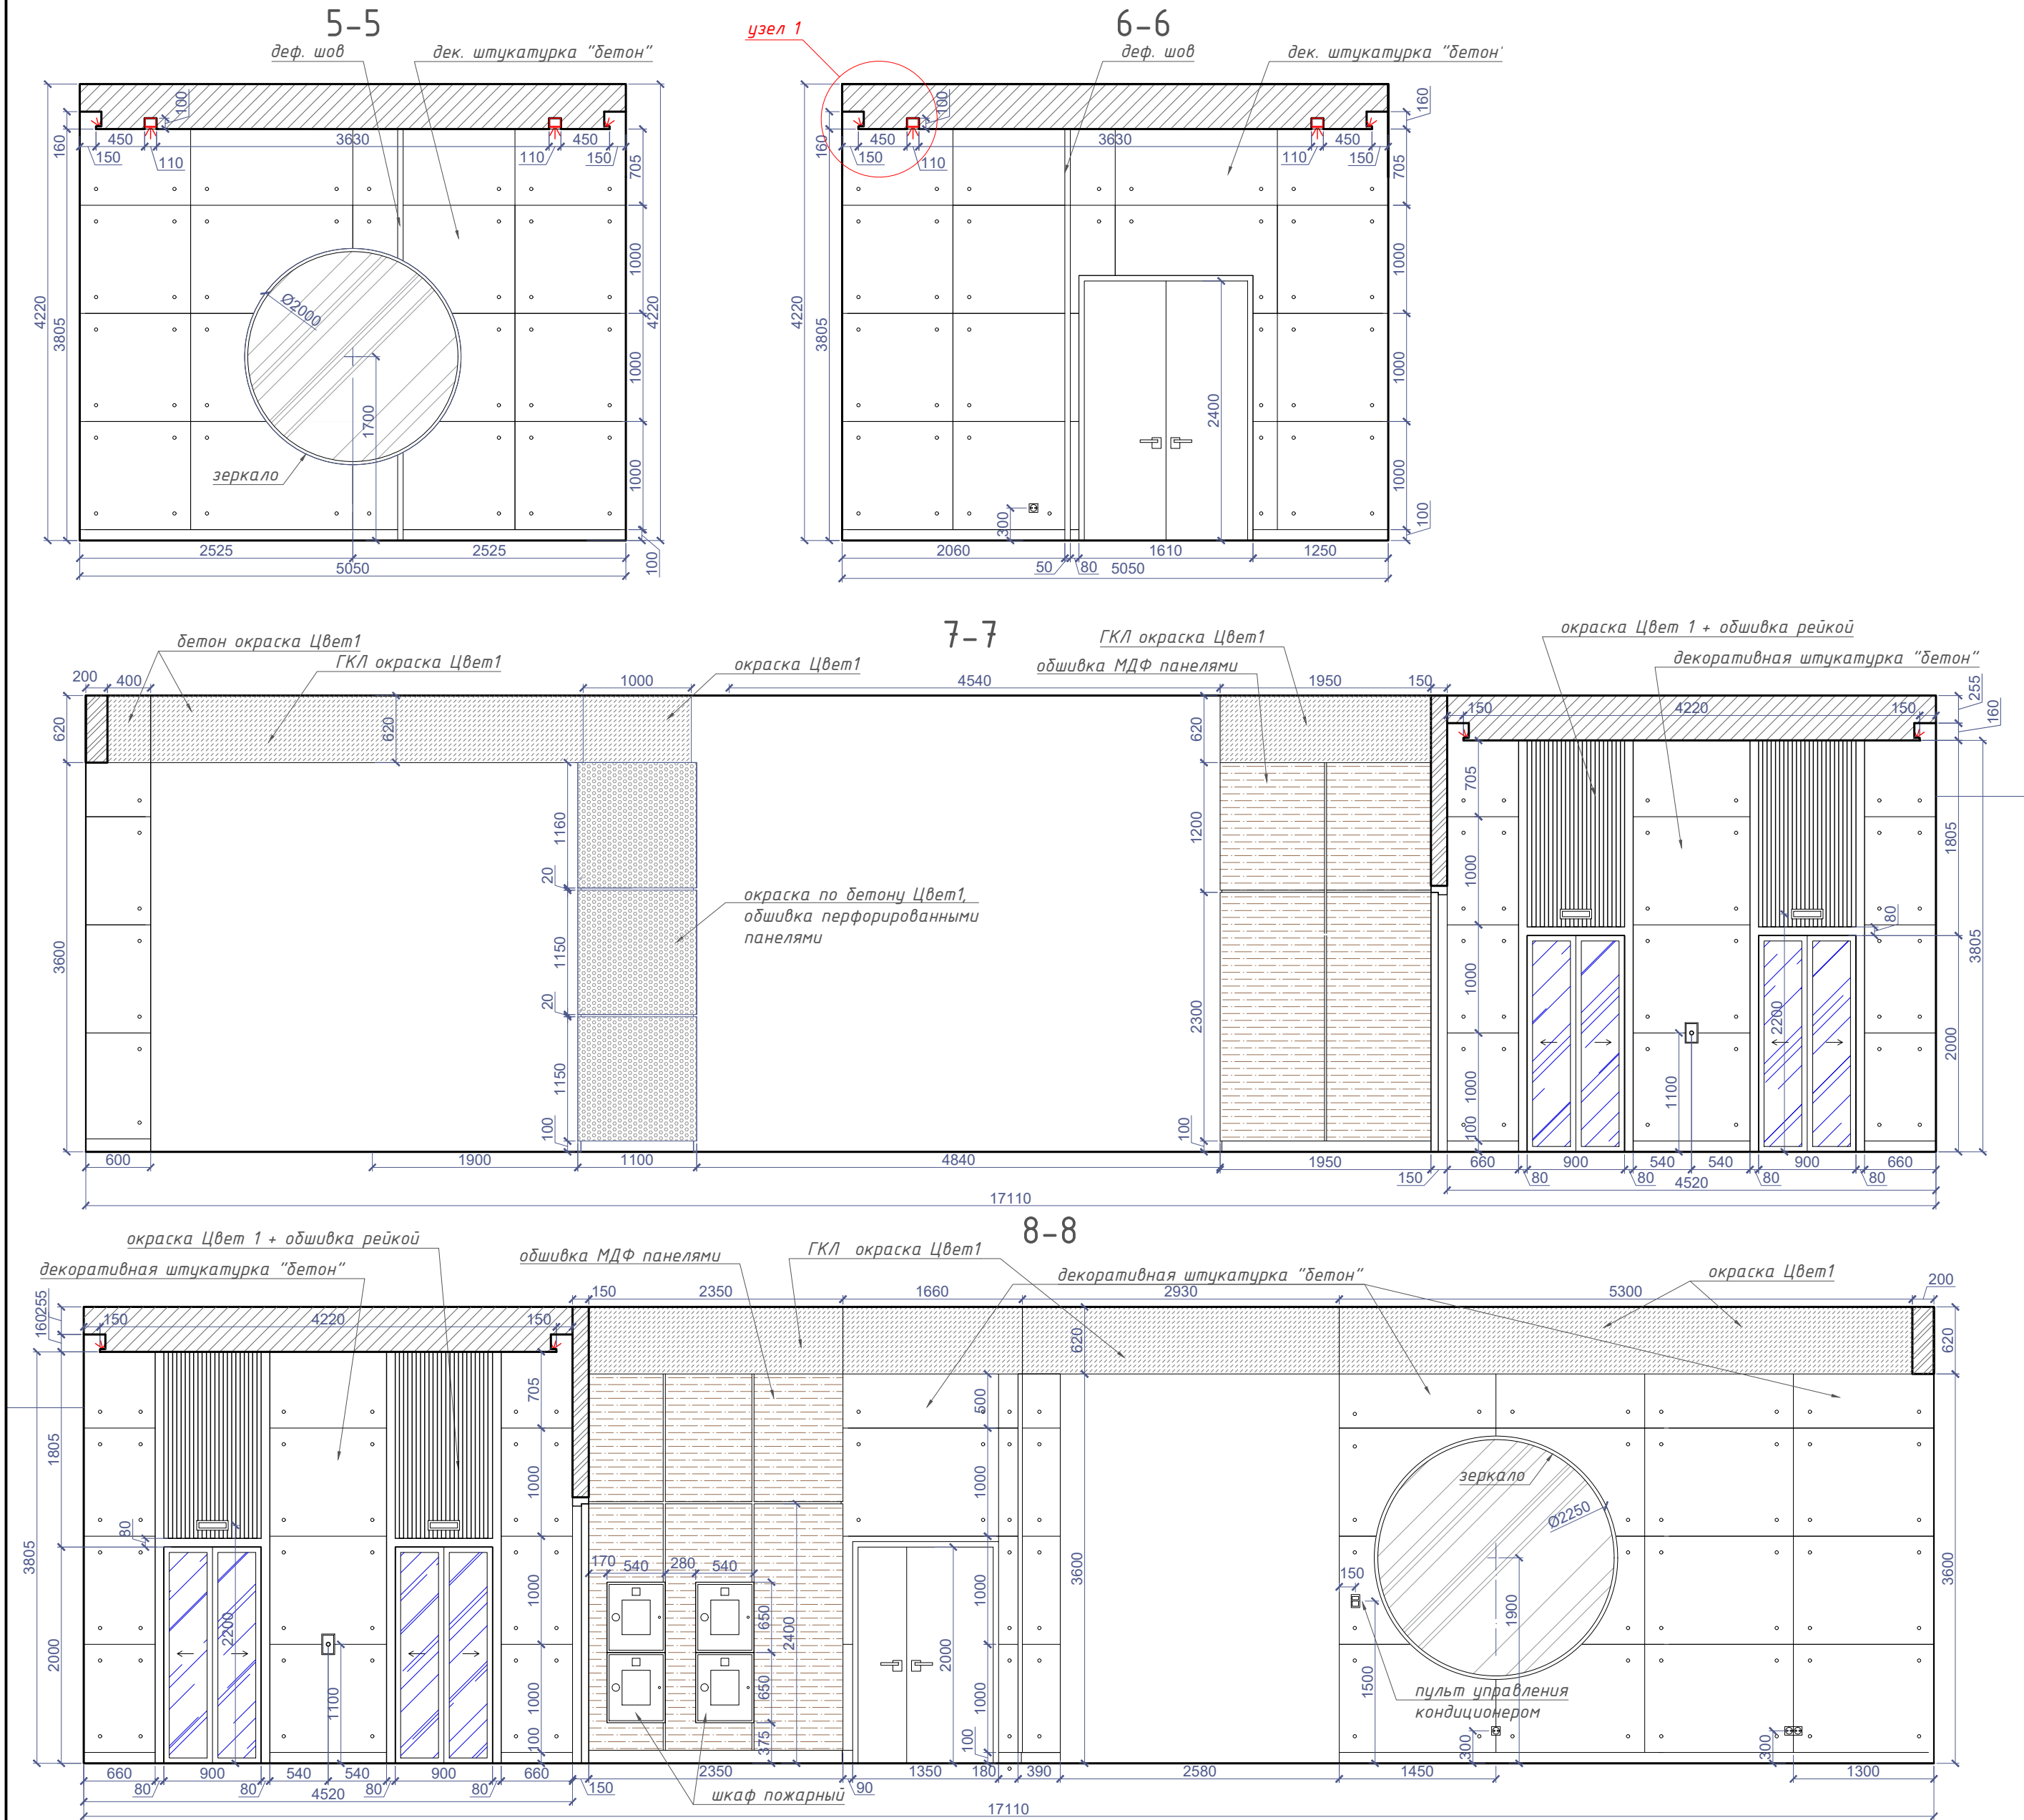

Указатель разверток

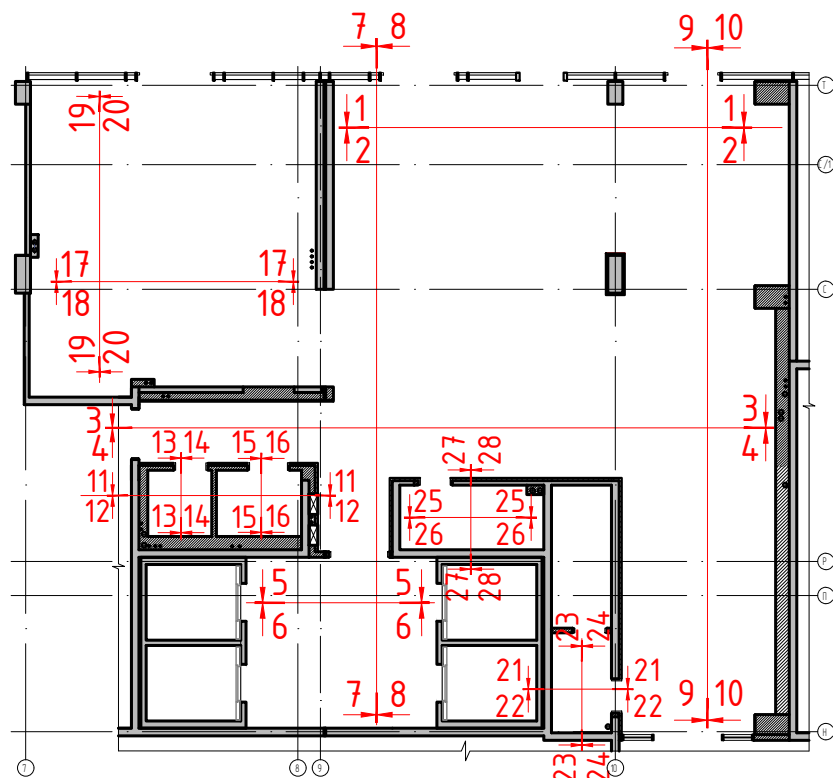

Узел 1 (М1:20)

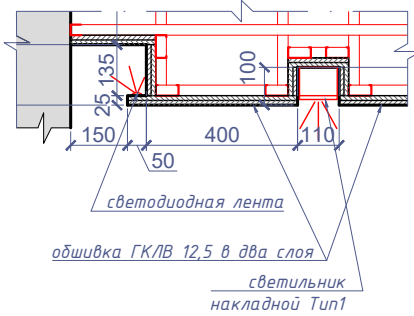












ПРИМЕЧАНИЯ:

1. План выполнен по черновым размерам помещений. Требуется корректировка размеров после проведения монтажных работ и чистой отделки!
2. Мебель на заказ устанавливается фирмой-изготовителем только после дополнительно снятых обмеров специалистами.
3. Цвета по RAL указаны условно, согласовать выкраски с дизайнеров производящим авторский надзор.
4. Размер и положение ревизионных люков уточнить по фактической необходимости.
5. Данный лист смотреть совместно с листом 3.

						05/2019г.	№ 041/АИ-0217							
						Объект: апартамент-отель. Адрес: г. Санкт-Петербург, ул. Херсонская д.43/12, лит. А								
Изм.	Колуч	Лист	№ док	Подпись	Дата	Интерьерные решения Холл-ресепшин			Стадия	Лист	Листов			
Ведущий арх-р	Быков М.М.								Р	15				
Диз-р	Терехин С.В.													
Диз-р						Развертки стен с 5-5 по 8-8. М 1:50			maxdesign					
Н контроль	Быков М.М.													

Развертки стен с 17-17 по 28-28. М 1:50

Указатель разверток

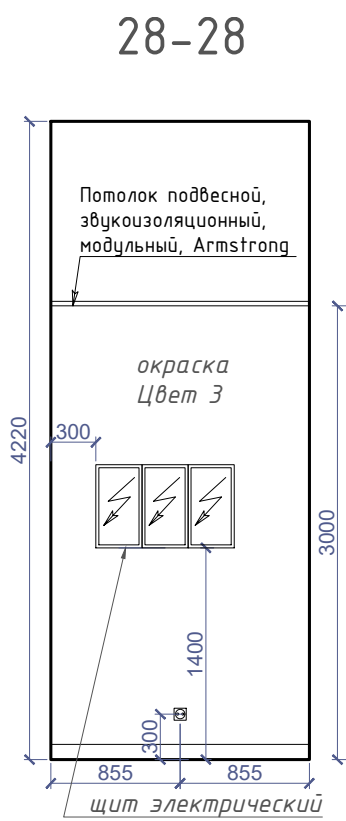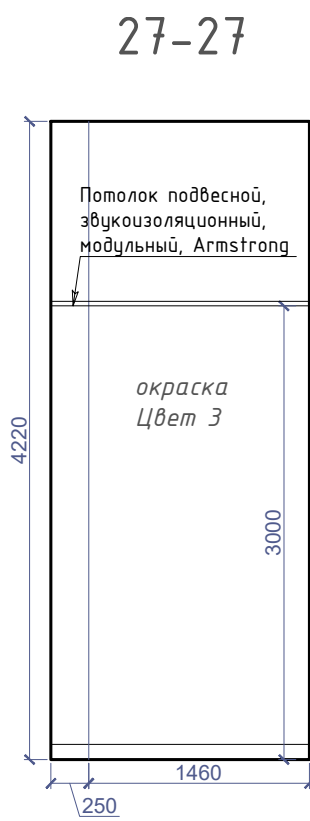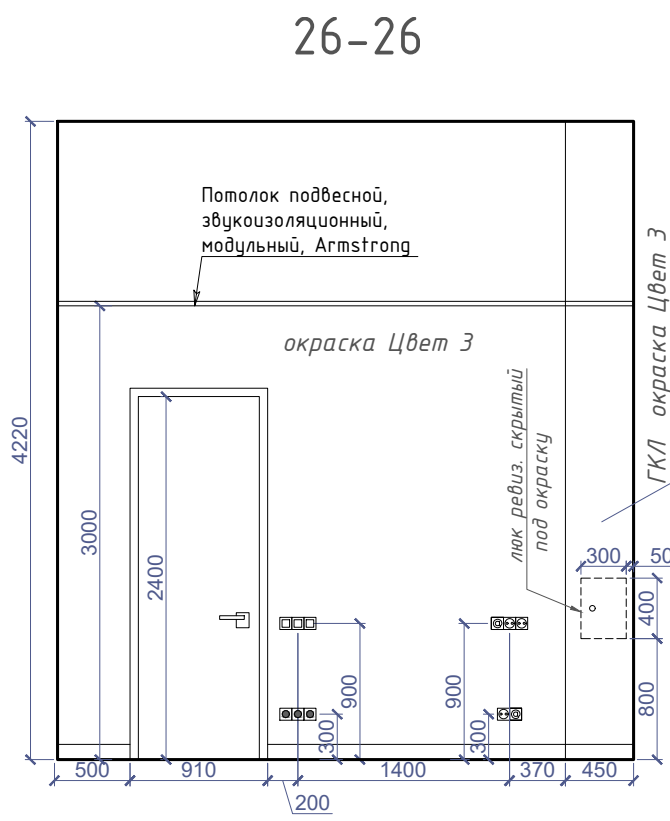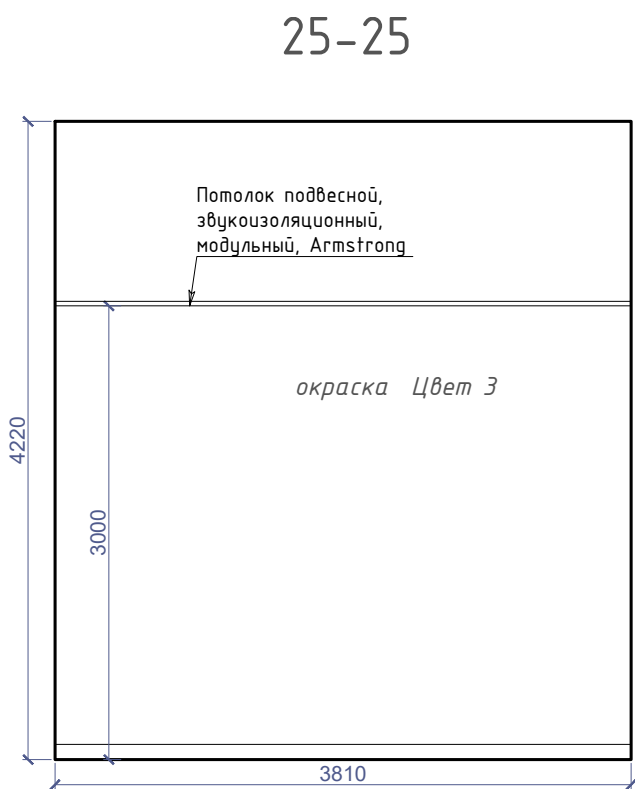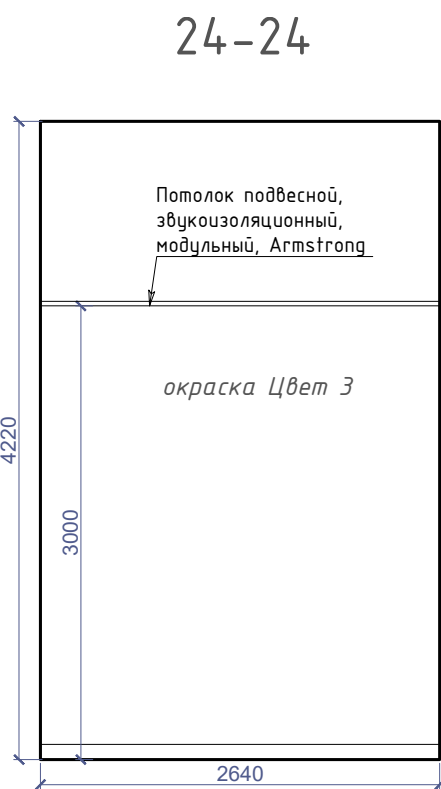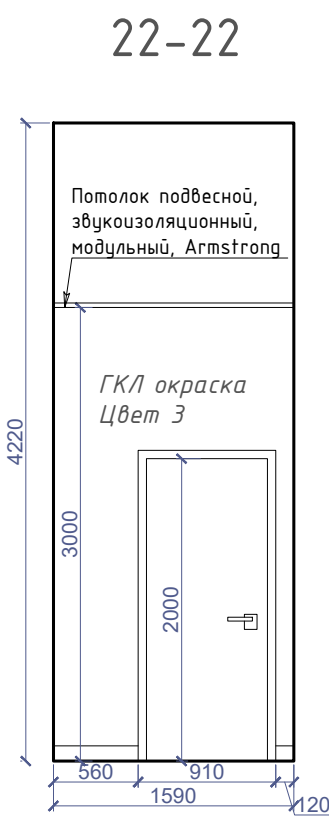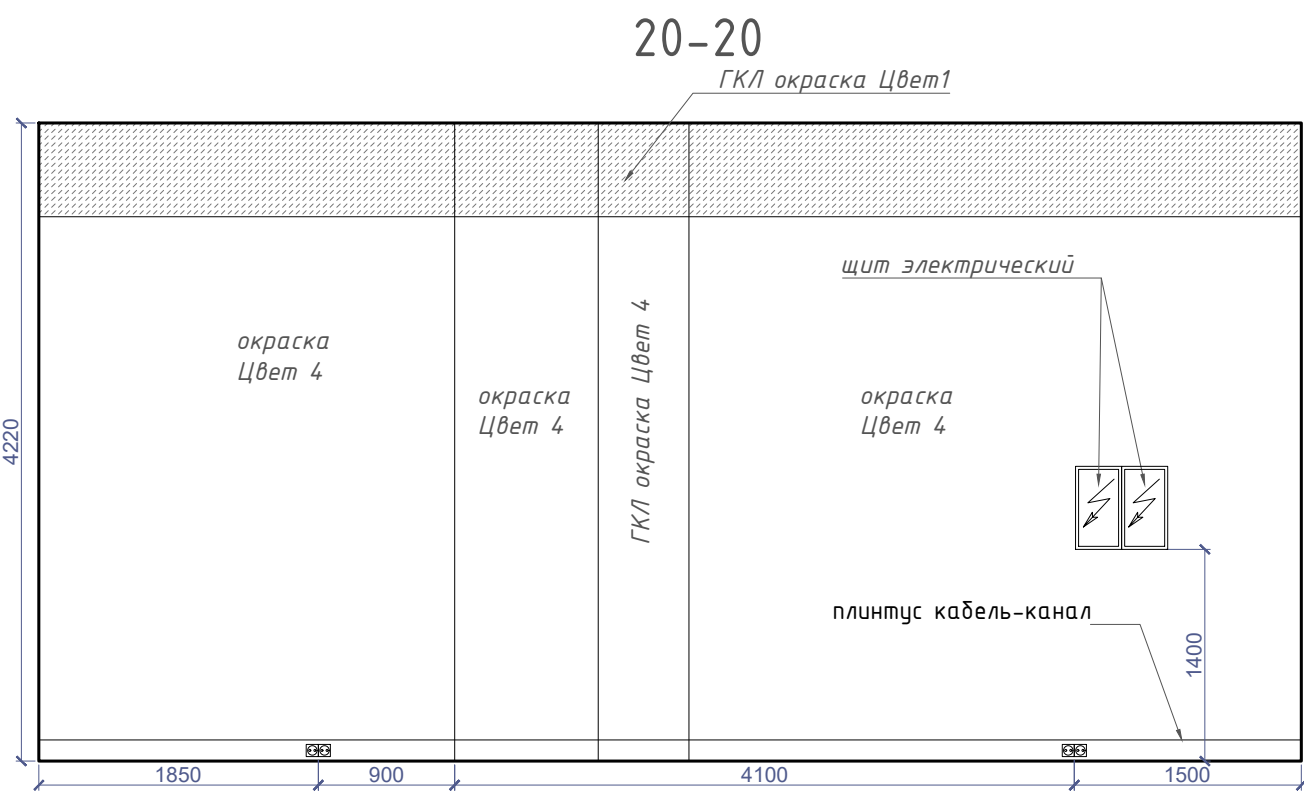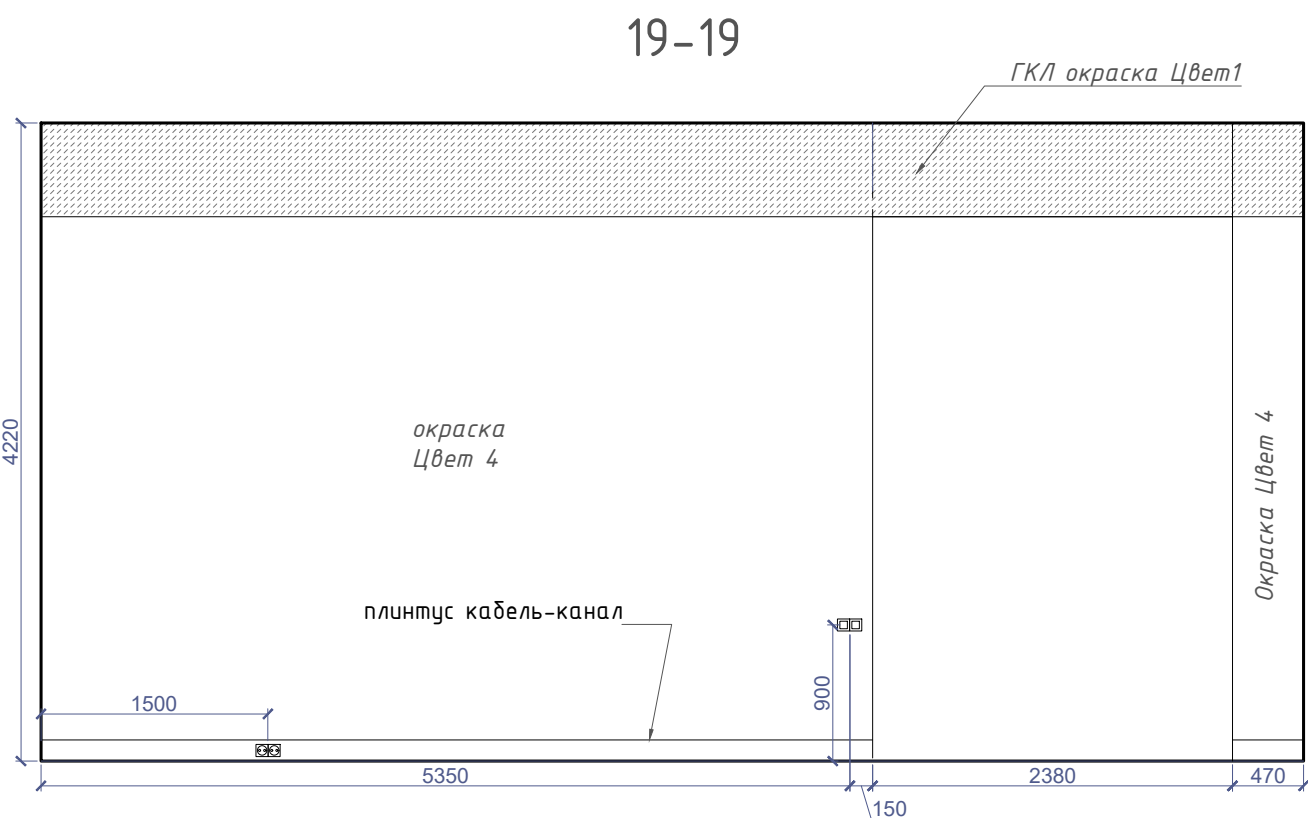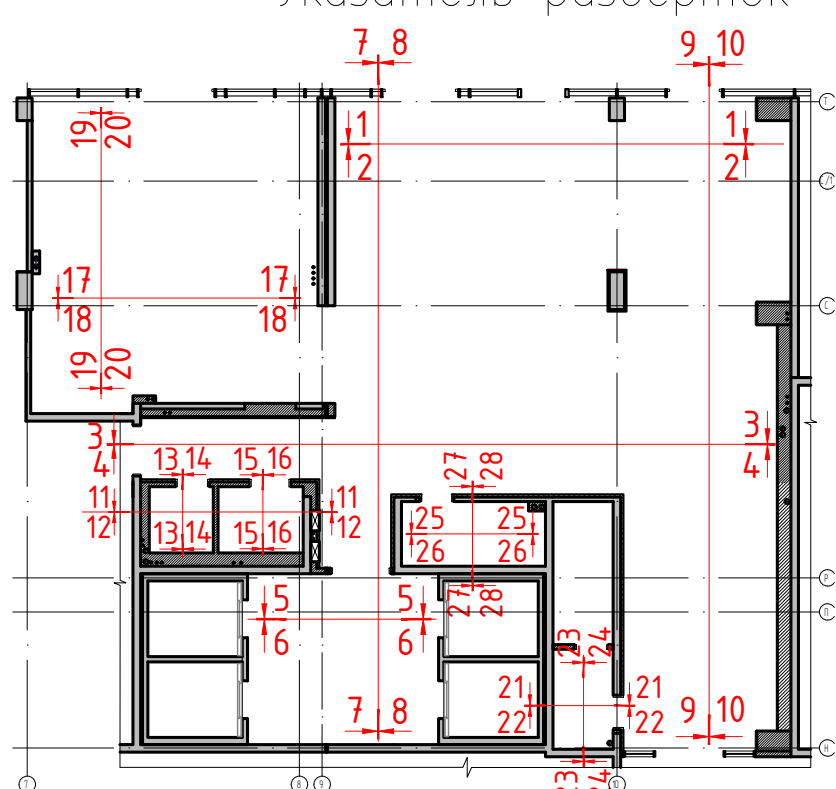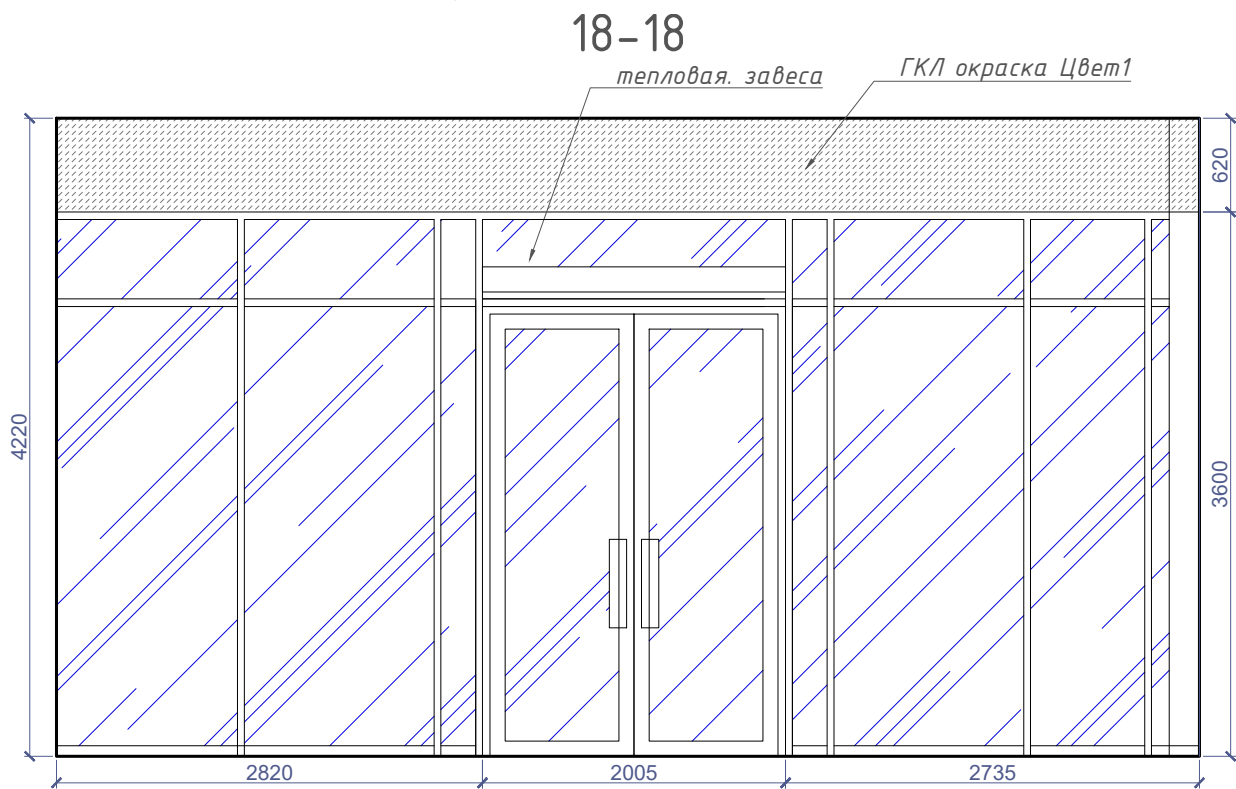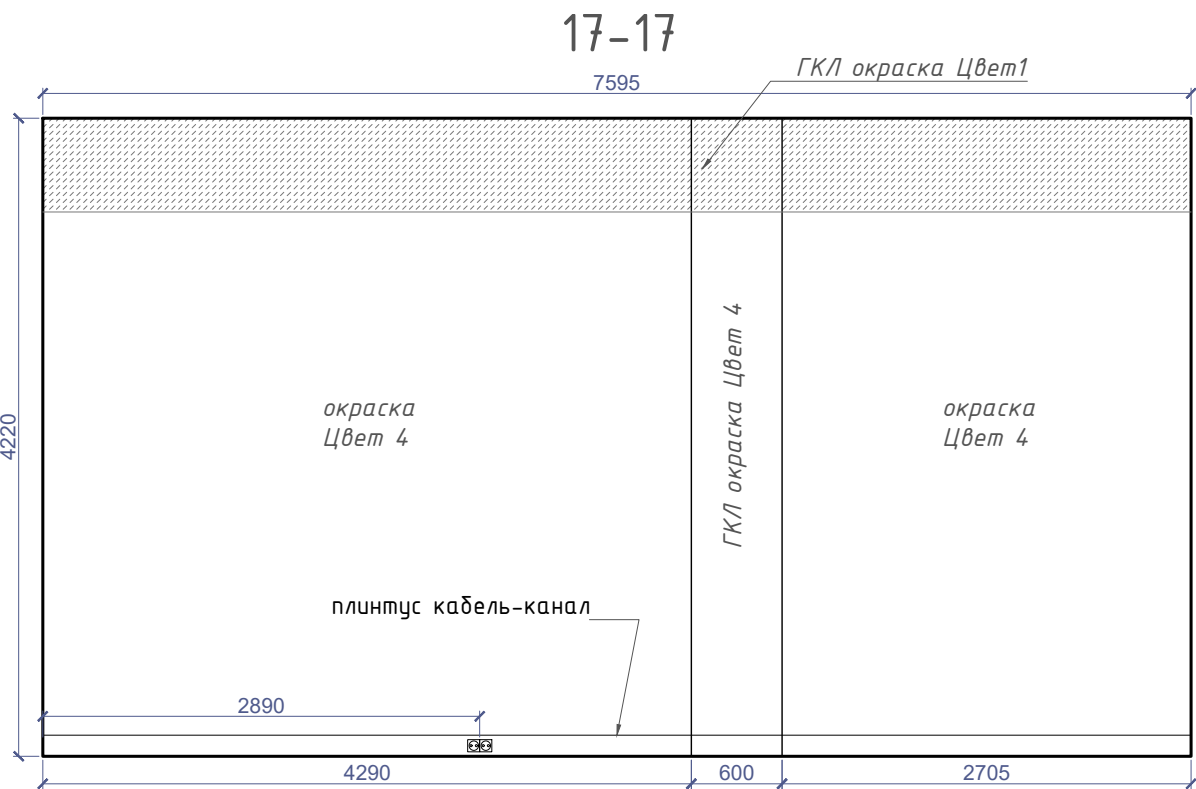


ПРИМЕЧАНИЯ:

- План выполнен по черновым размерам помещений. Требуется корректировка размеров после проведения монтажных работ и чистовой отделки!
- Цвета по RAL указаны условно, согласовать выкраски с ООО "МАКСДИЗАЙН".
- Смотровые люки уточнить по фактической необходимости.
- Данный лист смотреть совместно с листом 3 .

						05/2019г.	№ 041/ АИ-0217
						Объект: апартамент-отель. Адрес: г. Санкт-Петербург, ул. Херсонская д.43/12, лит. А	
Изм.	Колуч	Лист	№ док	Подпись	Дата	Интерьерные решения Холл-ресепшин	Стадия
Ведущий арх-р	Быков М.М.						Лист
Диз-р	Терехин С.В.						Листов
Диз-р							Р 17
						Развертки стен с 17-17 по 28-28.	
Н. контроль	Быков М.М.					maxdesign	

Обрамление лифтового портала. М 1:20

Общий вид портала

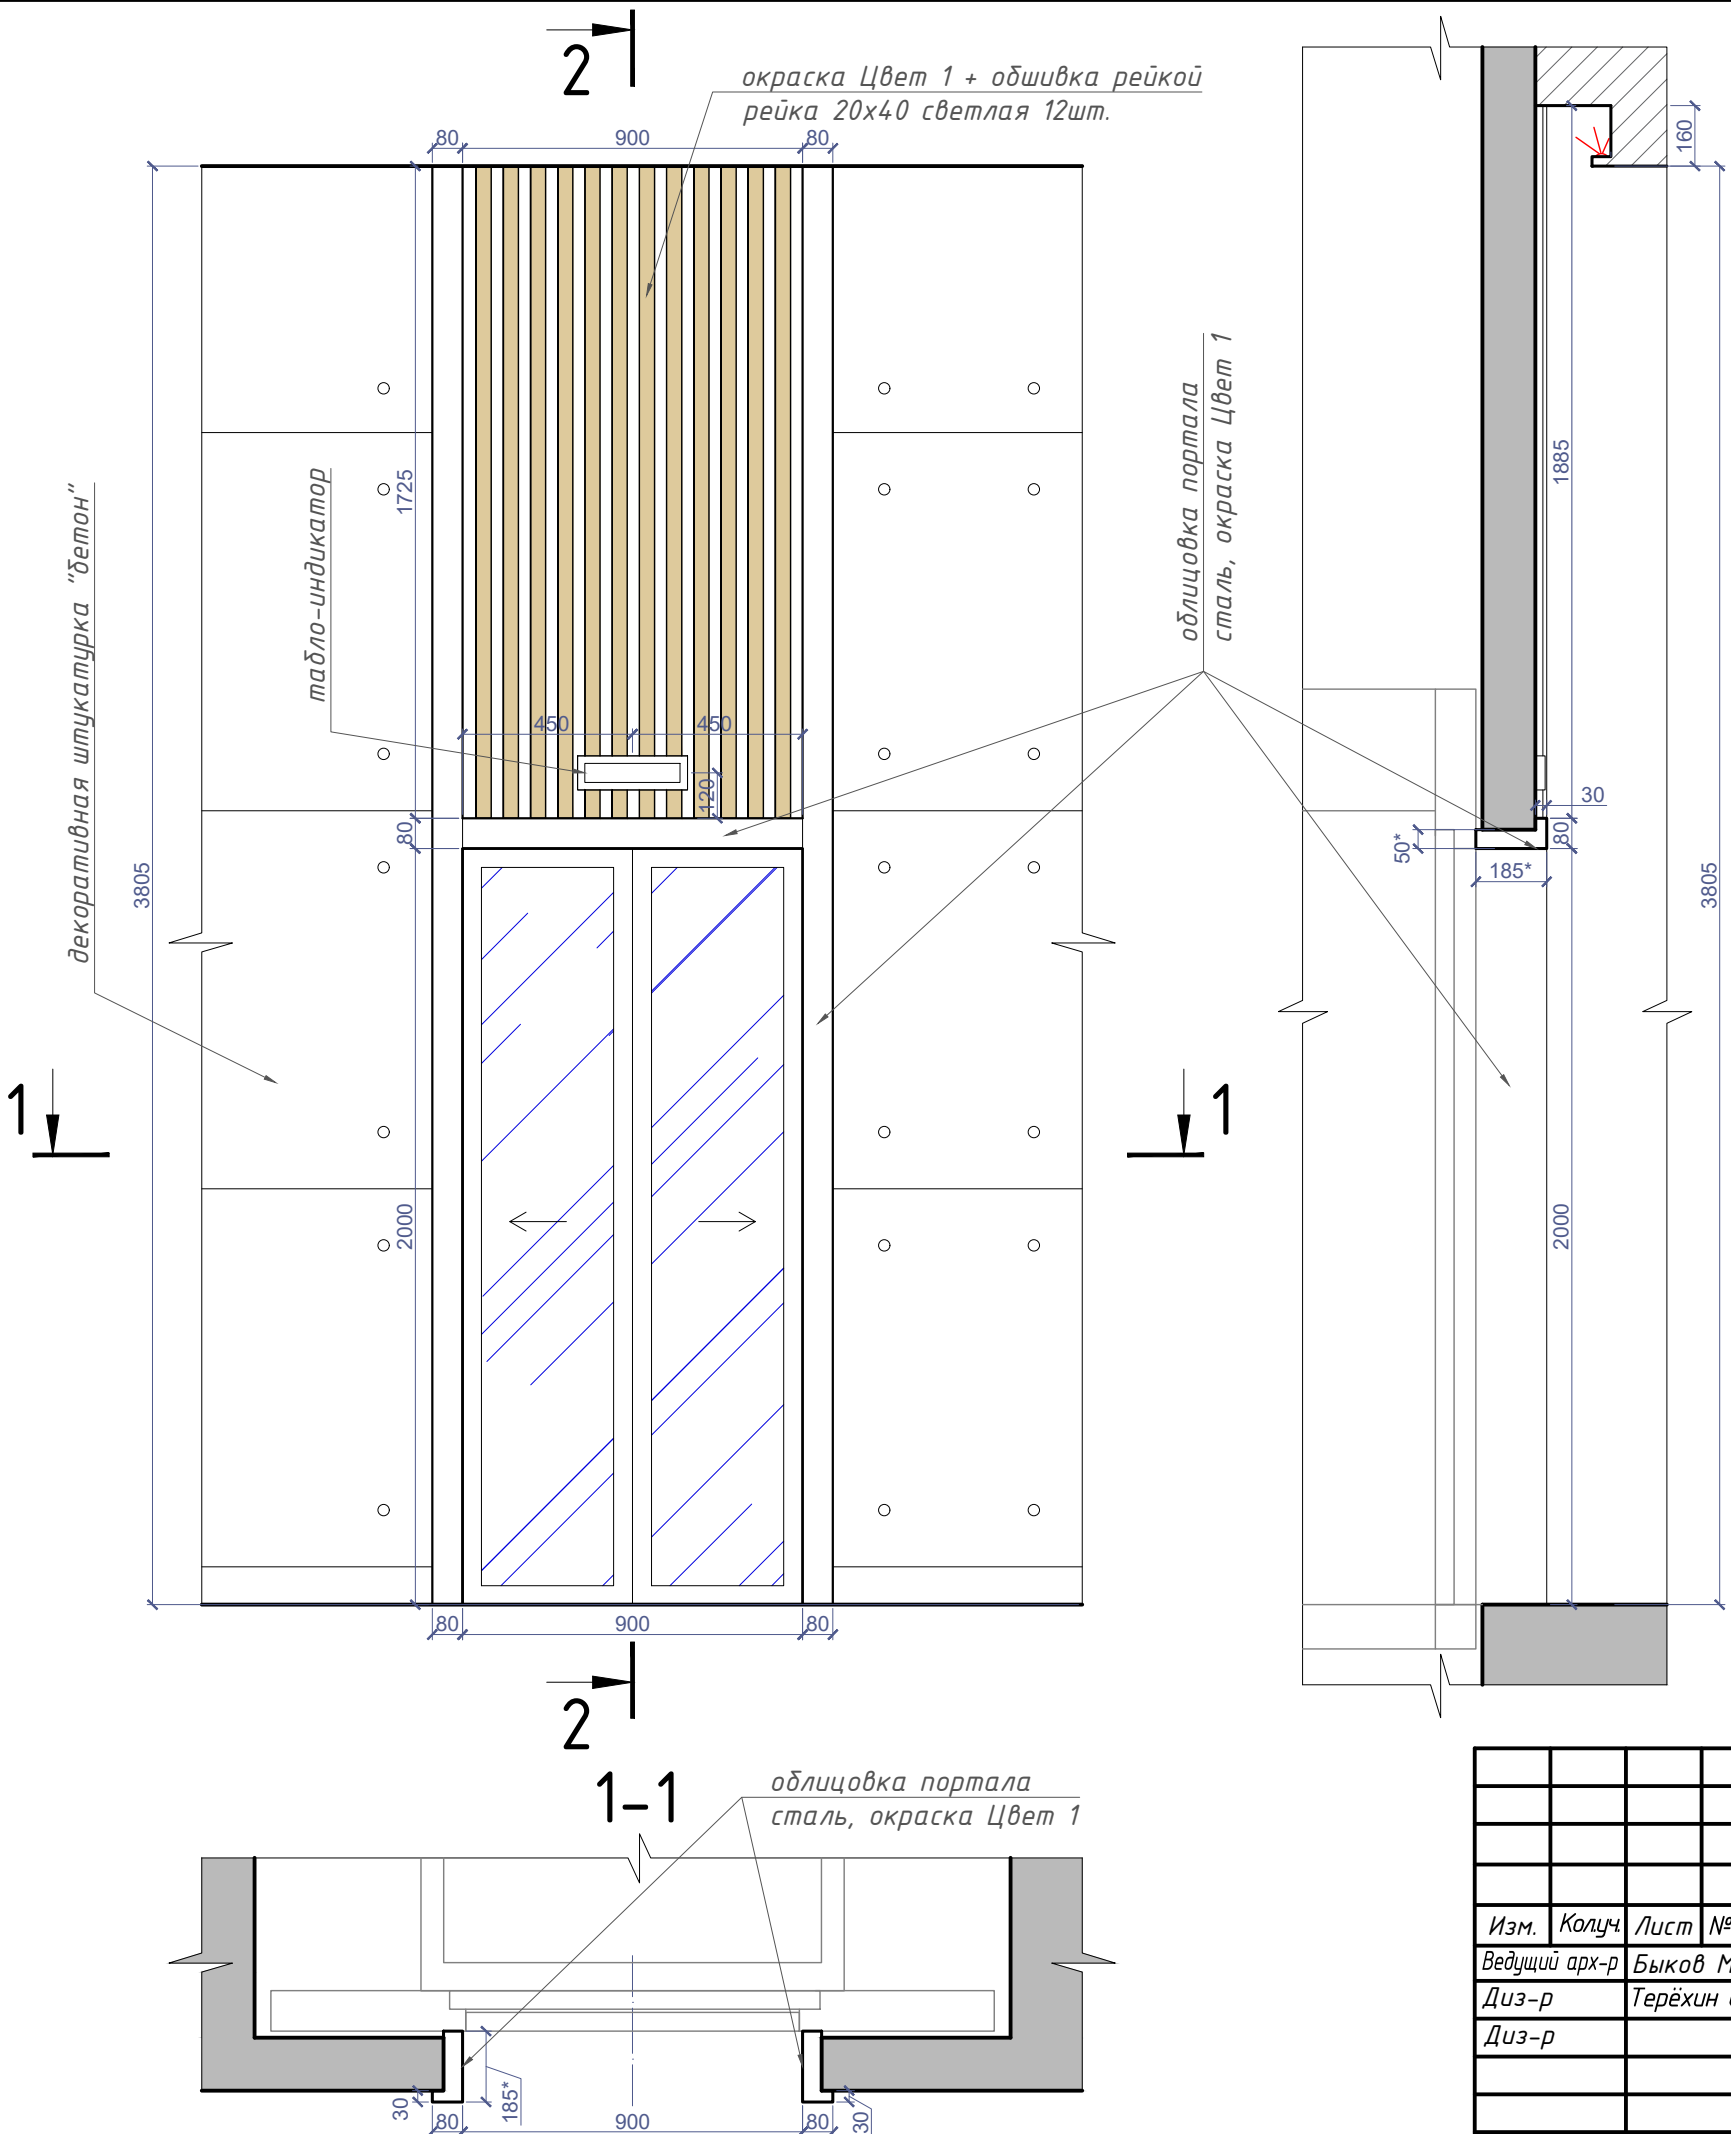

- ПРИМЕЧАНИЯ:
- 1. * – размеры для справок.
 - 2. Общее количество однотипных порталов на первый этаж – 4 шт.
 - 3. Метод крепежа и конструктивное исполнение выбирает изготовитель портала.
 - 4. Цвет портала RAL выбирает дизайнер ведущий авторский надзор.
 - 5. Приведенные размеры указаны от предчистовой отделки.

						05/2019г.			№041/АИ-0217			
						Объект: апарт-отель. Адрес: г. Санкт-Петербург, ул. Херсонская д.43/12, лит. А						
Изм.	Колуч	Лист	№ док	Подпись	Дата	Интерьерные решения Холл-ресепшн			Стадия	Лист	Листов	
Ведущий арх-р	Быков М.М.								Р	18		
Диз-р	Терёхин С.В.											
Диз-р						Обрамление лифтового портала.			maxdesign			
Н. контроль	Быков М.М.											


Ведомость заполнения дверных проемов.

Маркир.	Описание	Открывание	Размеры полотна (ШхВ)	Размеры проема (ШхВ)	Кол-во
ДГ-01	дверь скрытого монтажа, открывание наружу, глухая, МДФ	правая	800х2000	910х2080	1
ДГ-02		правая	1000х2000	1110х2080	1
ДГ-03	дверь скрытого монтажа, открывание наружу, глухая, МДФ	левая	800х2000	910х2080	1
ДГ-04	дверь глухая, деревянная	правая	800х2000	910х2080	1

ДП-1 EIW30	дверь противопожарная глухая	правая	1250х2080	1350х2080	1
ДП-2 EI30		правая	800х2080	910х2080	1
ДП-3 EI30		симметрич.	1500х2400	1610х2480	1

						05/2019г.			№ 04 1/ АИ-0217			
						Объект: апарт-отель. Адрес: г. Санкт-Петербург, ул. Херсонская д.43/12, лит. А						
Изм.	Колуч	Лист	№ док	Подпись	Дата	Интерьерные решения Холл-ресепшн			Стадия	Лист	Листов	
Ведущий арх-р	Быков М.М.								Р	19		
Диз-р	Терёхин С.В.											
Диз-р						Ведомость заполнения дверных проемов.			maxdesign			
Н. контроль	Быков М.М.											

Спецификация внутренних витражей.

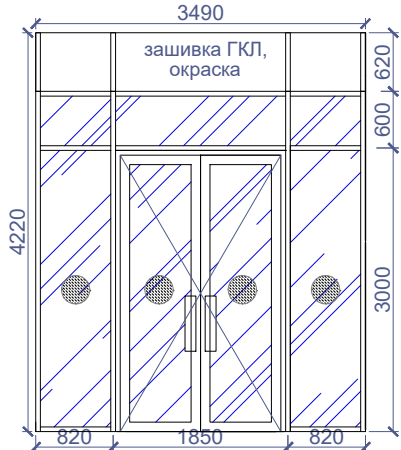Маркир.	Схема	Размеры проема (ШхВ)	Кол-во
ВВ-16		3490х4220	1

ПРИМЕЧАНИЯ:

- 1. Чертеж выполнен по черновым размерам помещений. Требуется корректировка размеров после проведения монтажных работ и чистовой отделки!
- 2. Изготовление и монтаж выполняется фирмой-изготовителем только после дополнительно снятых обмеров специалистами.
- 3. Чертеж смотреть совместно с листом 3.
- 4. Витраж ВВ-16 устанавливается на этапе 2 (вместо установленной на этапе 1 двери).

						05/2019г.			№ 041/АИ-0217			
						Объект: апарт-отель. Адрес: г. Санкт-Петербург, ул. Херсонская д.43/12, лит. А						
Изм.	Колуч	Лист	№ док.	Подпись	Дата	Интерьерные решения Холл-ресепшн	Стадия	Лист	Листов	maxdesign		
Ведущий арх-р	Быков М.М.						Р	20				
Диз-р	Терёхин С.В.											
Диз-р						Спецификация внутренних витражей.						
Н. контроль	Быков М.М.											

Спецификация оборудования и материалов

№	НАИМЕНОВАНИЕ	количес тво
Полы		
1	Керамогранит MILLENNIUM SILVER NAT RET 800X1600, 9мм	234 м2
2	Керамогранит 600х600 светлый, гр. износ. не менее PEI IV, коэф. скольжения не менее R11	8 м2
3	Керамогранит Италон Surfase Кортен, нарезка 800х90	87шт.
4	Латунь листовая 800х90	100шт.
5	Грязезащитное покрытие Emco diplomat 522G, 22мм	6,5 м2
6	Деформационный шов Deflex 446/b-050 h=15мм	11,5 м.п.
7	Плинтус дюрополимер h100мм, окраска в цвет 1	75 м.п.
8	Плинтусный кабель-канал SL 20х55, цвет RAL9011	22 м.п.
9	Профиль стыковки керамогранита	4 м.п.
Потолки		
10	Существующая м. плита, обеспылевание, окраска	214 м2
11	Потолок ГКЛ, окраска	39 м2
12		
13	Потолок подвесной, звукоизоляционный, модульный	11 м2
14	Деформационный шов	11,5 м.п.
Стены		
15	Роспись стен	31 м2
16	ГКЛ окраска	240 м2
17	Окраска	210 м2
18	МДФ панели	80 м2
19	Декоративная штукатурка "бетон"	104 м2
20	Обшивка декоративной рейкой	41 м2
21	Обшивка металлическими перфорированными панелями	11,5 м2
22	Керамическая плитка Тип 1 (мелкая, зеленая)	36 м2
23	Керамическая плитка Тип 2 (600х600)	17 м2
24	Деформационный шов Дефлекс 397	24 м.п.
Освещение		
25	Светильник Тип 1 (здесь и далее см. лист. 11 "План расположения осветительных приборов.")	20шт.
26	Светильник Тип 2	6шт.
27	Светильник Тип 3	22шт.
28	Светильник Тип 4	2шт.
29	Светильник Тип 5	1шт.
30	Светильник Тип 6	1шт.
31	Светильник Тип 7	9шт.
32	Светильник настенный Тип8	2шт.
33	Шина для установки светильников	40 м.п.
34	Светодиодная лента	41,5 м.п.
Электроарматура		
35	Розетка 220 вольт (здесь и далее Schneider Electric, серия - ATLAS DESIGN цвет - антрацит.)	26шт.
36	Розетка 220 вольт, встроена в плинтус кабель-канал	8шт.
37	Розетка RJ-45	6шт.
38	Розетка телефонная RJ-12	3шт.

39	Выключатель одноклавишный	5шт.
40	Встраиваемый в пол лючок для розеток на 2 розетки	1шт.
41	Кнопка вызова помощи для инвалидов	1шт.
42	Пульт управления кондиционером	1шт.
43	Кнопка вызова лифта	2шт.
44	Регулятор теплого пола	3шт.
45	Рамка одинарная	5шт.
46	Рамка двойная	7шт.
47	Рамка тройная	4шт.
48	Рамка четверная	3шт.
49	Пульт управления тепловой завесой	2шт.
Сантехника		
50	Унитаз подвесной с инсталляцией	2шт.
51	Раковина круглая - тумба	1шт.
52	Раковина круглая подвесная для инвалидов	1шт.
53	Смеситель для раковины из стены, бесконтактный	2шт.
54	Сушилка для рук Dyson Airblade V HU02 Nickel	2шт.
55	Диспенсер туалетной бумаги	2шт.
56	Раковина встраиваемая	1шт.
57	Смеситель для встраиваемой раковины	1шт.
58	Поручень раковины для инвалидов	1шт.
59	Поручень унитаза для инвалидов	1шт.
Мебель		
60	Диван 2400х1300х850h	2шт.
61	Стол журнальный	1шт.
62	Стойка продавца цветов	1шт.
63	Мебель продавца цветов	1шт.
64	Холодильник для цветов 2400х900	1шт.
65	Диван 2900х1100	3шт.
66	Стойка ресепшен	1шт.
67	Шкаф 1700х400	1шт.
68	Шкаф 1450х450	1шт.
69	Стол 1500х700	1шт.
70	Кресло офисное	3шт.
Люки скрытой установки		
72	Люк скрытый под окраску 400X400	3шт.
73	Люк скрытый под плитку 400X400	3шт.
74	Люк скрытый под окраску 300X400h	1шт.

ПРИМЕЧАНИЯ:

1. Все фактуры, тона и цвета согласовать с дизайнером ведущим авторский надзор.
2. Выбор и заказ мебели и оборудования заказчик осуществляет самостоятельно.

						05/2019г.			№041/АИ-0217					
						Объект: апарт-отель. Адрес: г. Санкт-Петербург, ул. Херсонская д.43/12, лит. А								
Изм.	Колуч	Лист	№ док	Подпись	Дата	Интерьерные решения Холл-ресепшн			Стадия	Лист	Листов			
Ведущий арх-р	Быков М.М.								Р	21				
Диз-р	Терёхин С.В.													
Диз-р						Спецификация оборудования и материалов			maxdesign					
Н. контроль	Быков М.М.													

Спецификация цветов

№ цвета в проекте	Номер по каталогу	ПРИМЕЧАНИЕ
1	DULUX 60RR 07/002	Потолок бетонный и все коммуникации, верх стен, облицовка лифта, плинтусы, стены за рейкой, ниши потолочные для светильников, низ шпонированных дверей
2	RAL 9003	Потолок светлый ГКЛ
3	RAL 7044	Стены офиса и помещения багажа
4	RAL 7047	Стены коммерческого помещения

						05/2019г.		№041/АИ-0217	
						Объект: апарт-отель. Адрес: г. Санкт-Петербург, ул. Херсонская д.43/12, лит. А			
Изм.	Колуч	Лист	№ док	Подпись	Дата	Интерьерные решения Холл-ресепшн	Стадия	Лист	Листов
Ведущий арх-р	Быков М.М.						Р	1	
Диз-р	Терёхин С.В.								
Диз-р						Спецификация цветов	maxdesign		
Н контроль	Быков М.М.								